National System Operator (Pvt) Ltd
Sri Lanka

POWER SYSTEM STRENGTHENING AND RENEWABLE ENERGY INTEGRATION PROJECT
(ADB LOAN NO: 4548-SRI)

PACKAGE 6

Procurement of Plant

Design, Supply, and Installation

Single-Stage: Two-Envelope
Bidding Procedure

BIDDING DOCUMENT
FOR

Integration of Renewable Energy Management System (REMS) and NSCC SCADA/EMS Modernization

VOLUME 6 of 8
Part II- REQUIREMENTS
Section 6 - Employer's Requirements: Part C-Drawings

Issued on: March 30, 2026
Invitation for Bids No.: CEB/AGM(P)/TDE/IFB/2025/02/HLPC
OCB No.: CEB/AGM(P)/TDE/OCB/2025/02/HLPC
Employer: National System Operator (Pvt) Ltd
Country: Sri Lanka

© Director Engineering, NTNSP

Office of the Director (System Control)
National System Operator (Pvt) Ltd,
No. 80, Parliament Road,
Pelawatta, Battaramulla.
Sri Lanka.
Document – Revision 1

Information Copy

Information Copy

Preface

This Bidding Document for Procurement of Plant – Design, Supply, and Installation, has been prepared by National Transmission Network Service Provider (Private) Limited and is based on the Standard Bidding Document for Procurement of Plant – Design, Supply, and Installation (SBD Plant) issued by the Asian Development Bank dated December 2021.

ADB's SBD Plant has the structure and the provisions of the Master Procurement Document entitled "Procurement of Plant – Design, Supply, and Installation", prepared by multilateral development banks and other public international financial institutions except where ADB-specific considerations have required a change.

In this Bidding Document, any reference to 'Ceylon Electricity Board' shall be deemed to refer to 'National System Operator (Pvt) Ltd.' Similarly, any reference to 'CEB' shall be deemed to refer to 'NSO'.

Information Copy

Information Copy

Table of Contents - Summary Description

VOLUME 1 OF 8

PART I BIDDING PROCEDURES

Section 1 - Instructions to Bidders (ITB) ---------- 1-1
This Section specifies the procedures to be followed by Bidders in the preparation and submission of their Bids. Information is also provided on the submission, opening, and evaluation of bids and on the award of contract.

Section 2 - Bid Data Sheet (BDS) ---------- 2-1
This Section consists of provisions that are specific to each procurement and supplement the information or requirements included in Section 1 - Instructions to Bidders.

Section 3 -Evaluation and Qualification Criteria (EQC) ---------- 3-1
This Section contains the bid evaluation criteria to determine the lowest evaluated bid and lists the necessary qualifications of Bidders.

VOLUME 2 OF 8

PART I BIDDING PROCEDURES

Section 4 -Bidding Forms (BDF) ---------- 4A-1
Part A-Price Bid
This Section contains the forms which are to be completed by the Bidder and submitted as part of its Bid.

VOLUME 3 OF 8

PART I BIDDING PROCEDURES

Section 4 -Bidding Forms (BDF) ---------- 4B-1
Part B-Technical Bid
This Section contains the forms which are to be completed by the Bidder and submitted as part of its Bid.

Section 5 -Eligible Countries (ELC) ---------- 5-1
This Section contains the list of eligible countries.

VOLUME 4 OF 8

PART II REQUIREMENTS

Section 6 -Employer's Requirements (ERQ) ---------- 6A-1
Part A-Scope of Works

VOLUME 5 OF 8

PART II REQUIREMENTS

Section 6 -Employer's Requirements (ERQ) ---------- 6B-1
Part B-Technical Specification

Information Copy

VOLUME 6 OF 8

PART II REQUIREMENTS

Section 6 -Employer's Requirements (ERQ) ---------- 6C-1
Part C-Drawings

VOLUME 7 OF 8

PART II REQUIREMENTS

Section 6 -Employer's Requirements (ERQ) ---------- 6D-1
Part D-Supplementary Information
Section 6 -Employer's Requirements (ERQ) ---------- 6D-1
Part E-Bank Guarantees and Certificates, Change Orders

VOLUME 8 OF 8

PART III CONDITIONS OF CONTRACT AND CONTRACT FORMS

Section 7 -General Conditions of Contract (GCC) ---------- 7-1
This Section contains the general clauses to be applied in all contracts. These Conditions are subject to the variations and additions set out in Section 8 (Special Conditions of Contract).

Section 8 -Special Conditions of Contract (SCC) ---------- 8-1
This Section contains provisions that are specific to each contract and that modify or supplement the GCC. Whenever there is a conflict, the provisions herein shall prevail over those in the GCC. The clause number of the SCC is the corresponding clause number of the GCC.

Section 9 -Contract Forms (COF) ---------- 9-1
This Section contains forms, which, once completed, will form part of the Contract. The forms for Performance Security and Advance Payment Security, when required, shall only be completed by the successful Bidder after contract award.

Information Copy

Information Copy

Information Copy

Property of NTNSP Director Engineering

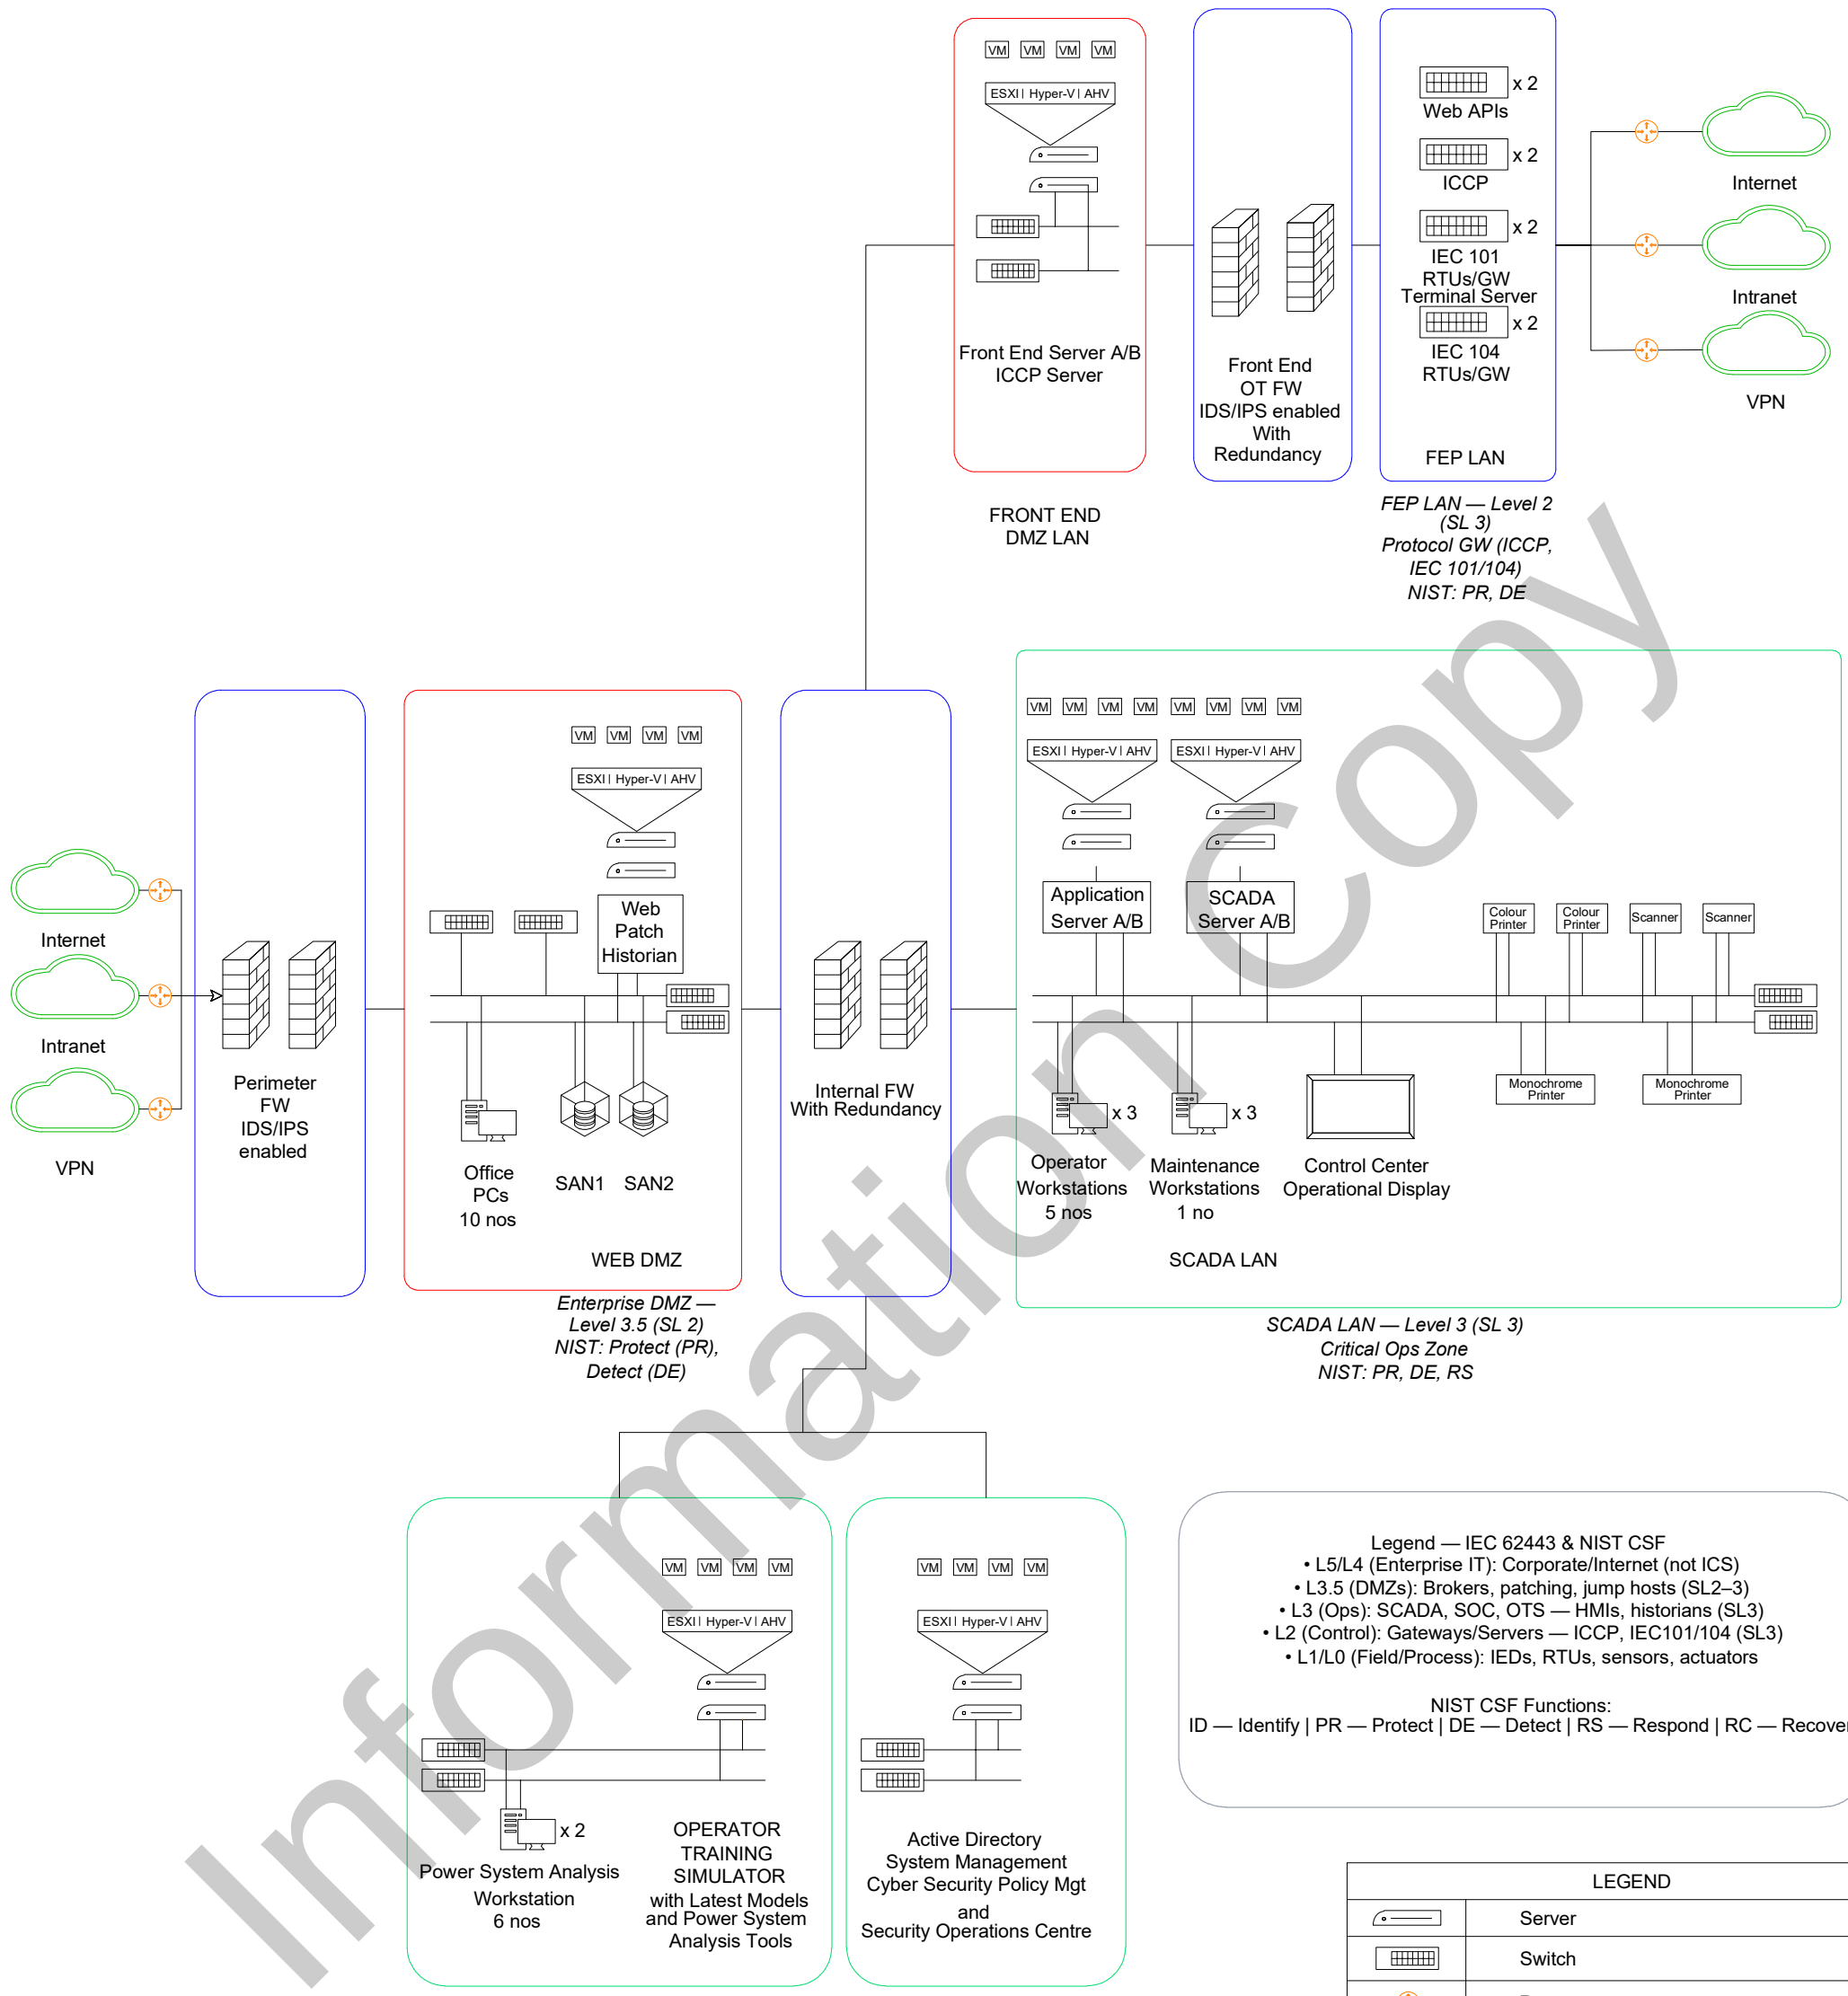

Legend — IEC 62443 & NIST CSF
- L5/L4 (Enterprise IT): Corporate/Internet (not ICS)
- L3.5 (DMZs): Brokers, patching, jump hosts (SL2–3)
- L3 (Ops): SCADA, SOC, OTS — HMIs, historians (SL3)
- L2 (Control): Gateways/Servers — ICCP, IEC101/104 (SL3)
- L1/L0 (Field/Process): IEDs, RTUs, sensors, actuators

NIST CSF Functions:
ID — Identify | PR — Protect | DE — Detect | RS — Respond | RC — Recover

LEGEND	
	Server
	Switch
	Router
	Firewall
x 3	Operator Workstation with 3 displays
x 2	Power System Analysis Workstation with 2 displays
	Office PC with 1 display

Minimum requirements are identified in the diagrams.

Information Copy

NATIONAL TRANSMISSION NETWORK SERVICE PROVIDER (PVT) LTD
DIRECTOR ENGINEERING

Project Title
POWER SYSTEM STRENGTHENING AND RENEWABLE ENERGY INTEGRATION PROJECT (PSSREIP)
PACKAGE 6

Drawing Title
Proposed Network Diagram with Firewall Isolation and Cybersecurity Zones

Rev. No.	Date	Description	Drawn	Checked	Approved

Funding Agency: ADB

Scale - NTS
Size - A3
Sheet 01 of 01
Rev. Date
Rev. 0

Released for: Tendering ✓ / Construction

Dwg. No. TD/CE/1/273/D/01

		Signature	Date
Drawn	Sandamali		18.03.2026
Designed	Kasun		
Checked			
Approved			

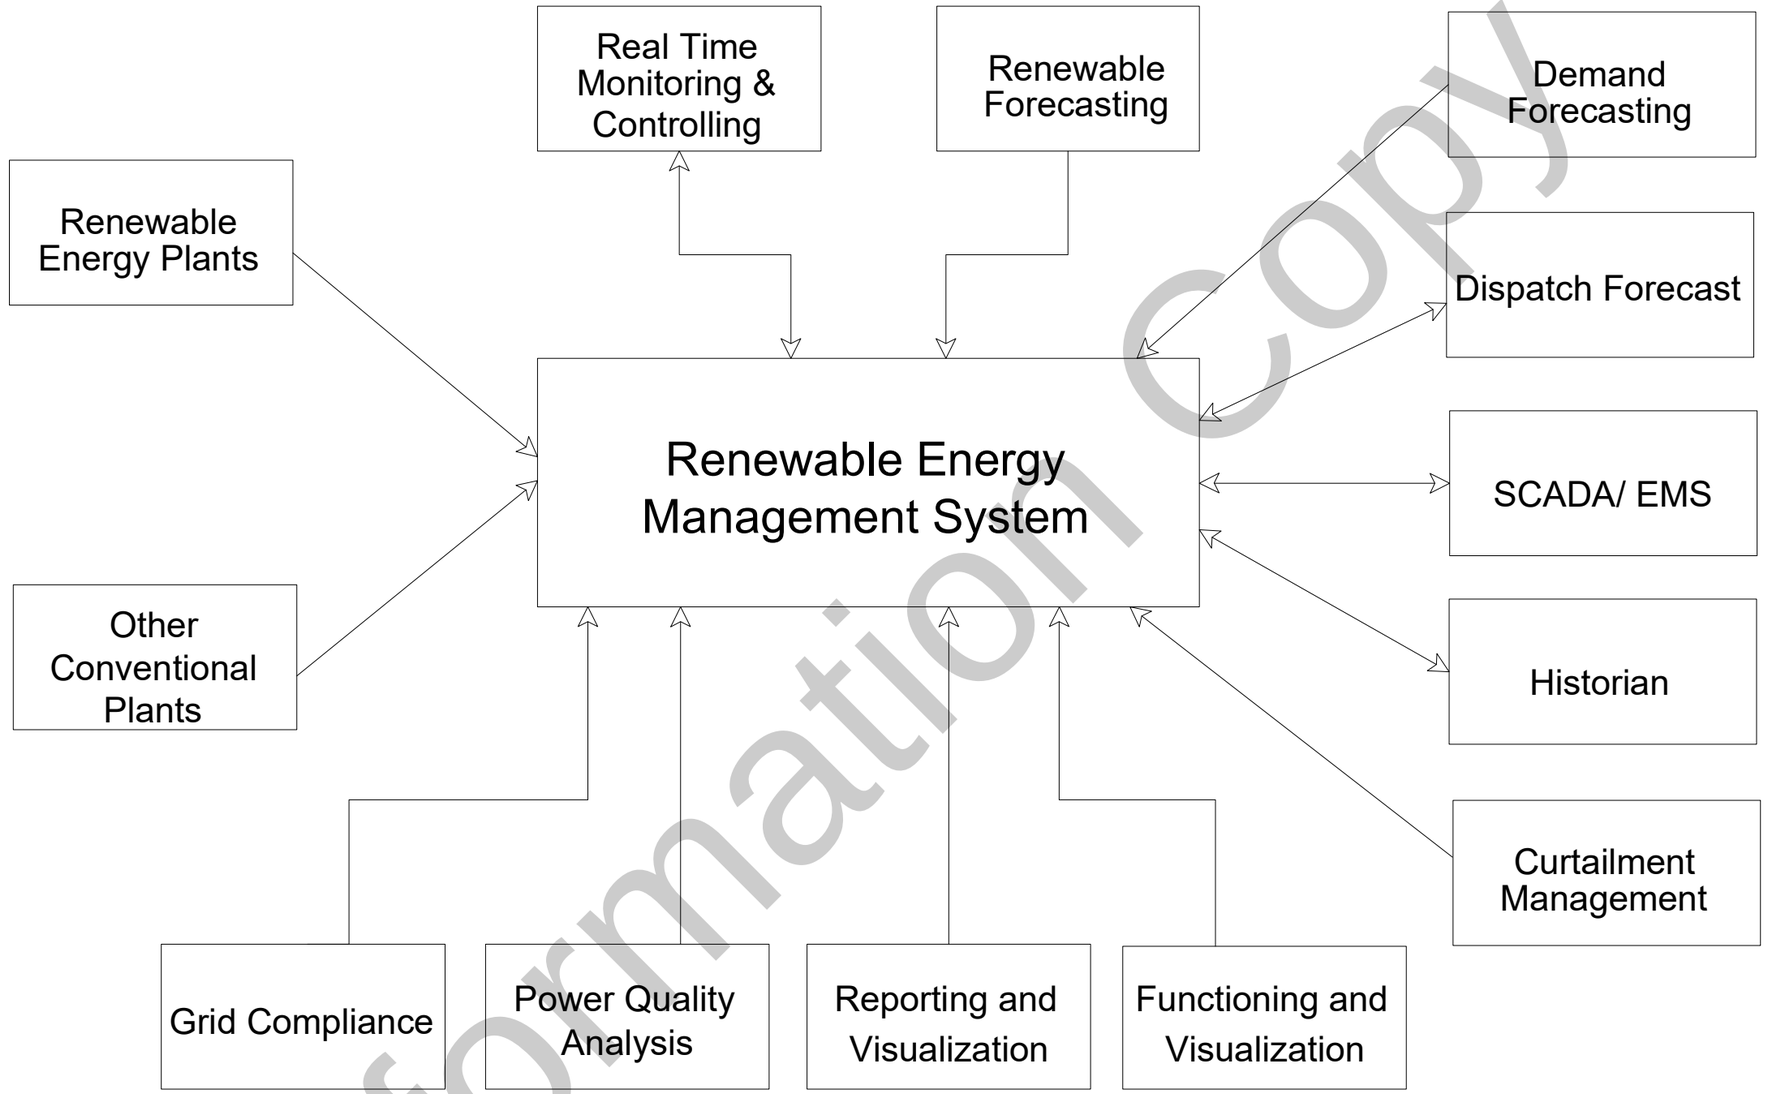

Minimum requirements are identified in the diagrams.

Information copy

Property of NTNSP Director Engineering

Revision Record					
Rev. No.	Date	Description	Drawn	Checked	Approved

NTNSP NATIONAL TRANSMISSION NETWORK SERVICE PROVIDER (PRIVATE) LIMITED

NATIONAL TRANSMISSION NETWORK SERVICE PROVIDER (PVT) LTD
DIRECTOR ENGINEERING

Project Title
POWER SYSTEM STRENGTHENING AND RENEWABLE ENERGY INTEGRATION PROJECT (PSSREIP) PACKAGE 6

Funding Agency
ADB

Drawing Title
RENEWABLE ENERGY MANAGEMENT SYSTEM (REMS)

Scale -	NTS			Rev. Date	
Size -	A3				
Sheet	01	of	01	Rev.	0
Dwg. No.	TD/CE/1/273/D/02				

		Signature	Date
Drawn	Sandamali		18.03.2026
Designed	Kasun		
Checked			
Approved			

Released for		
	Tendering	✓
	Construction	

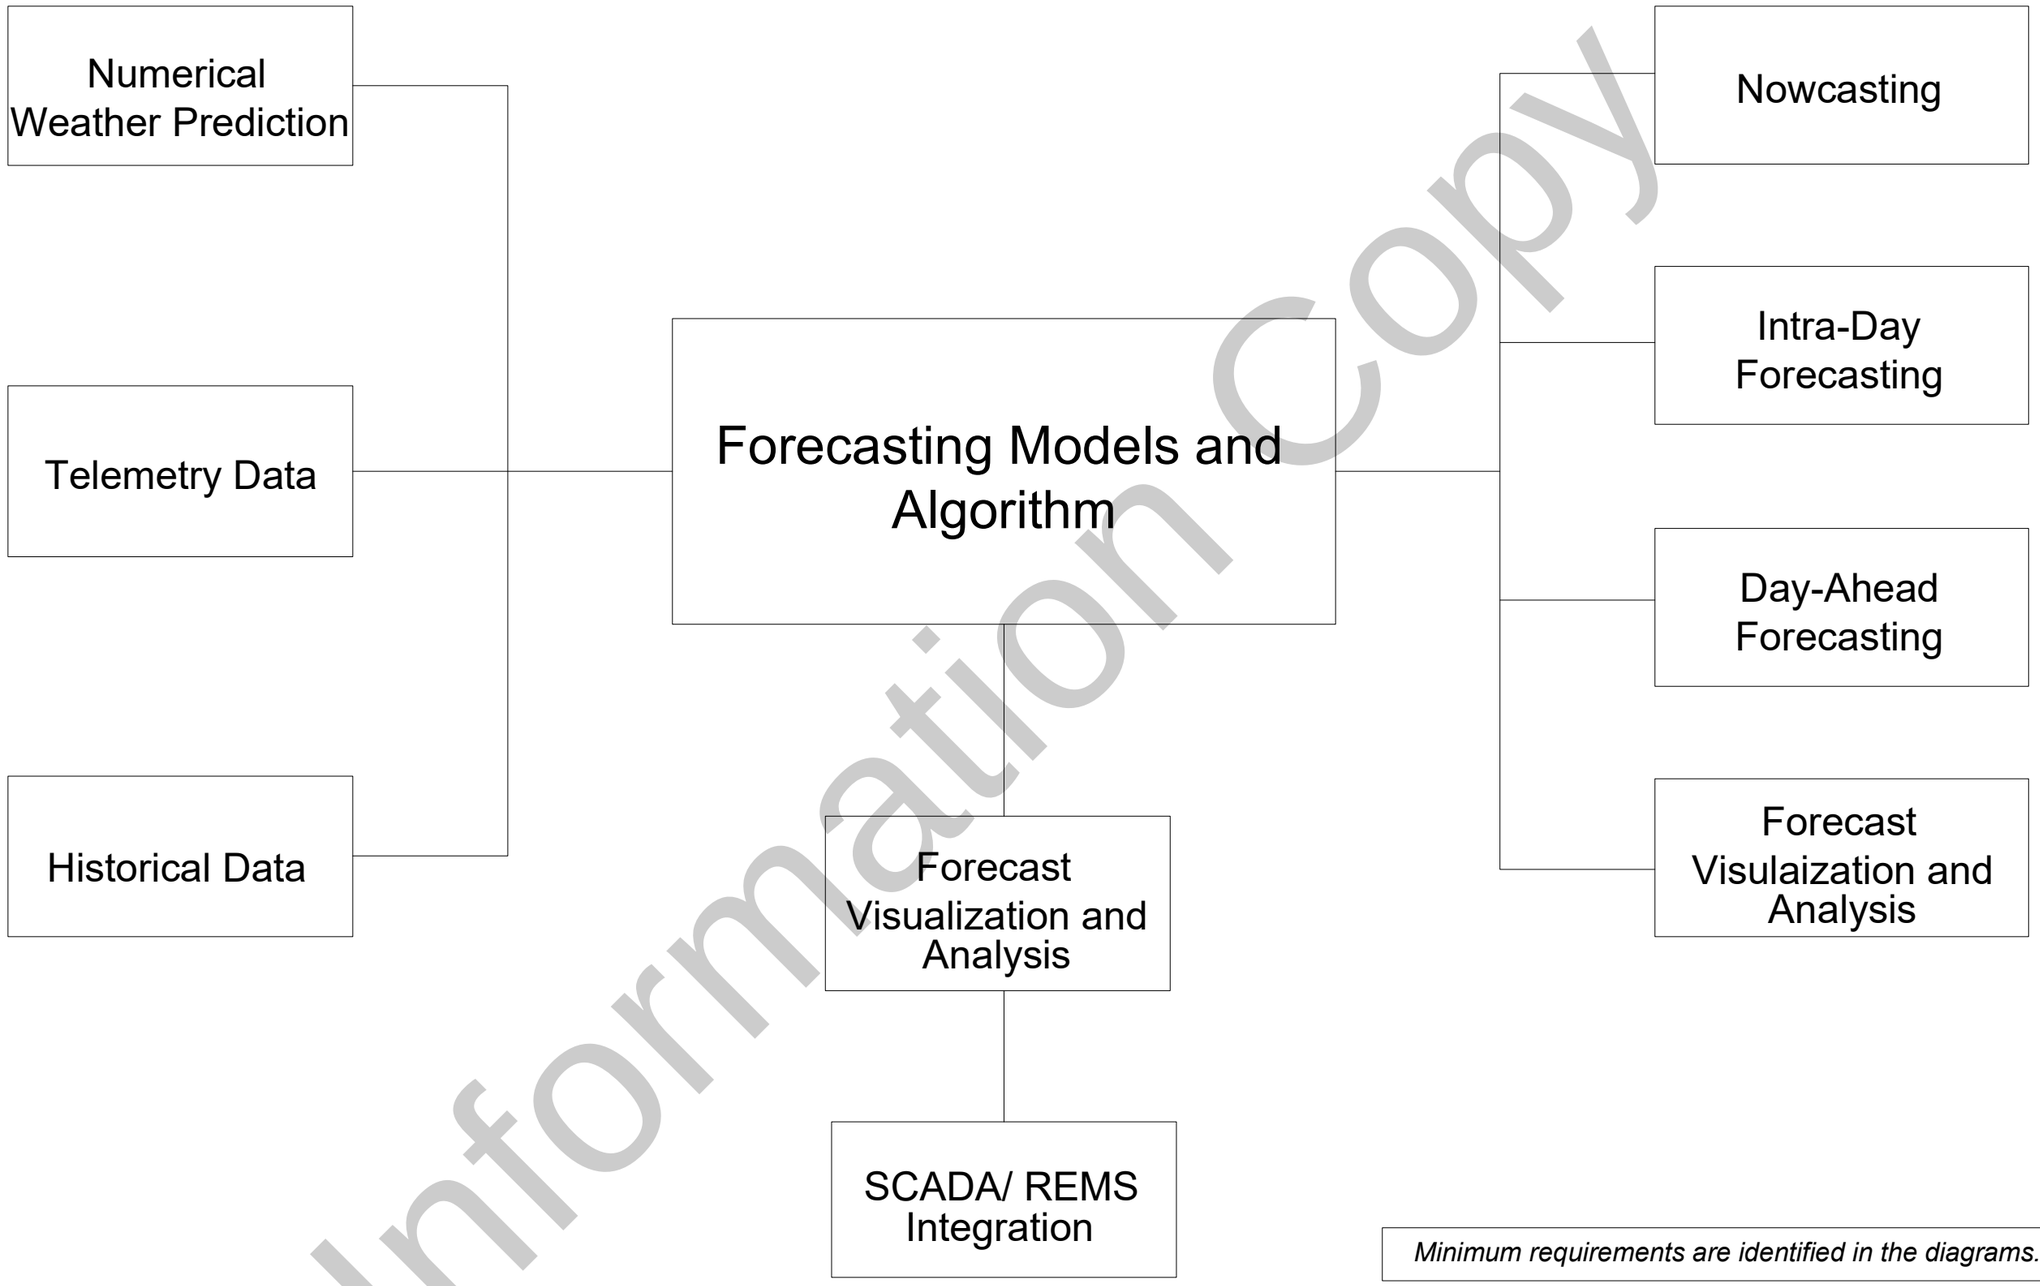

Minimum requirements are identified in the diagrams.

Information Copy

Property of NTNSP Director Engineering

Property of NTNSP Director Engineering

Revision Record					
Rev. No.	Date	Description	Drawn	Checked	Approved

NTNSP NATIONAL TRANSMISSION NETWORK SERVICE PROVIDER (PRIVATE) LIMITED

NATIONAL TRANSMISSION NETWORK SERVICE PROVIDER (PVT) LTD
DIRECTOR ENGINEERING

Project Title
POWER SYSTEM STRENGTHENING AND RENEWABLE ENERGY INTEGRATION PROJECT (PSSREIP) PACKAGE 6

Funding Agency
ADB

Drawing Title
RENEWABLE ENERGY FORECASTING SYSTEM

Scale - NTS			Rev. Date		
Size - A3					
Sheet 01 of 01			Rev. 0		
Dwg. No. TD/CE/1/273/D/03					

	Signature		Date
Drawn	Sandamali		18.03.2026
Designed	Kasun		
Checked			
Approved			

Released for: Tendering ✓ ; Construction

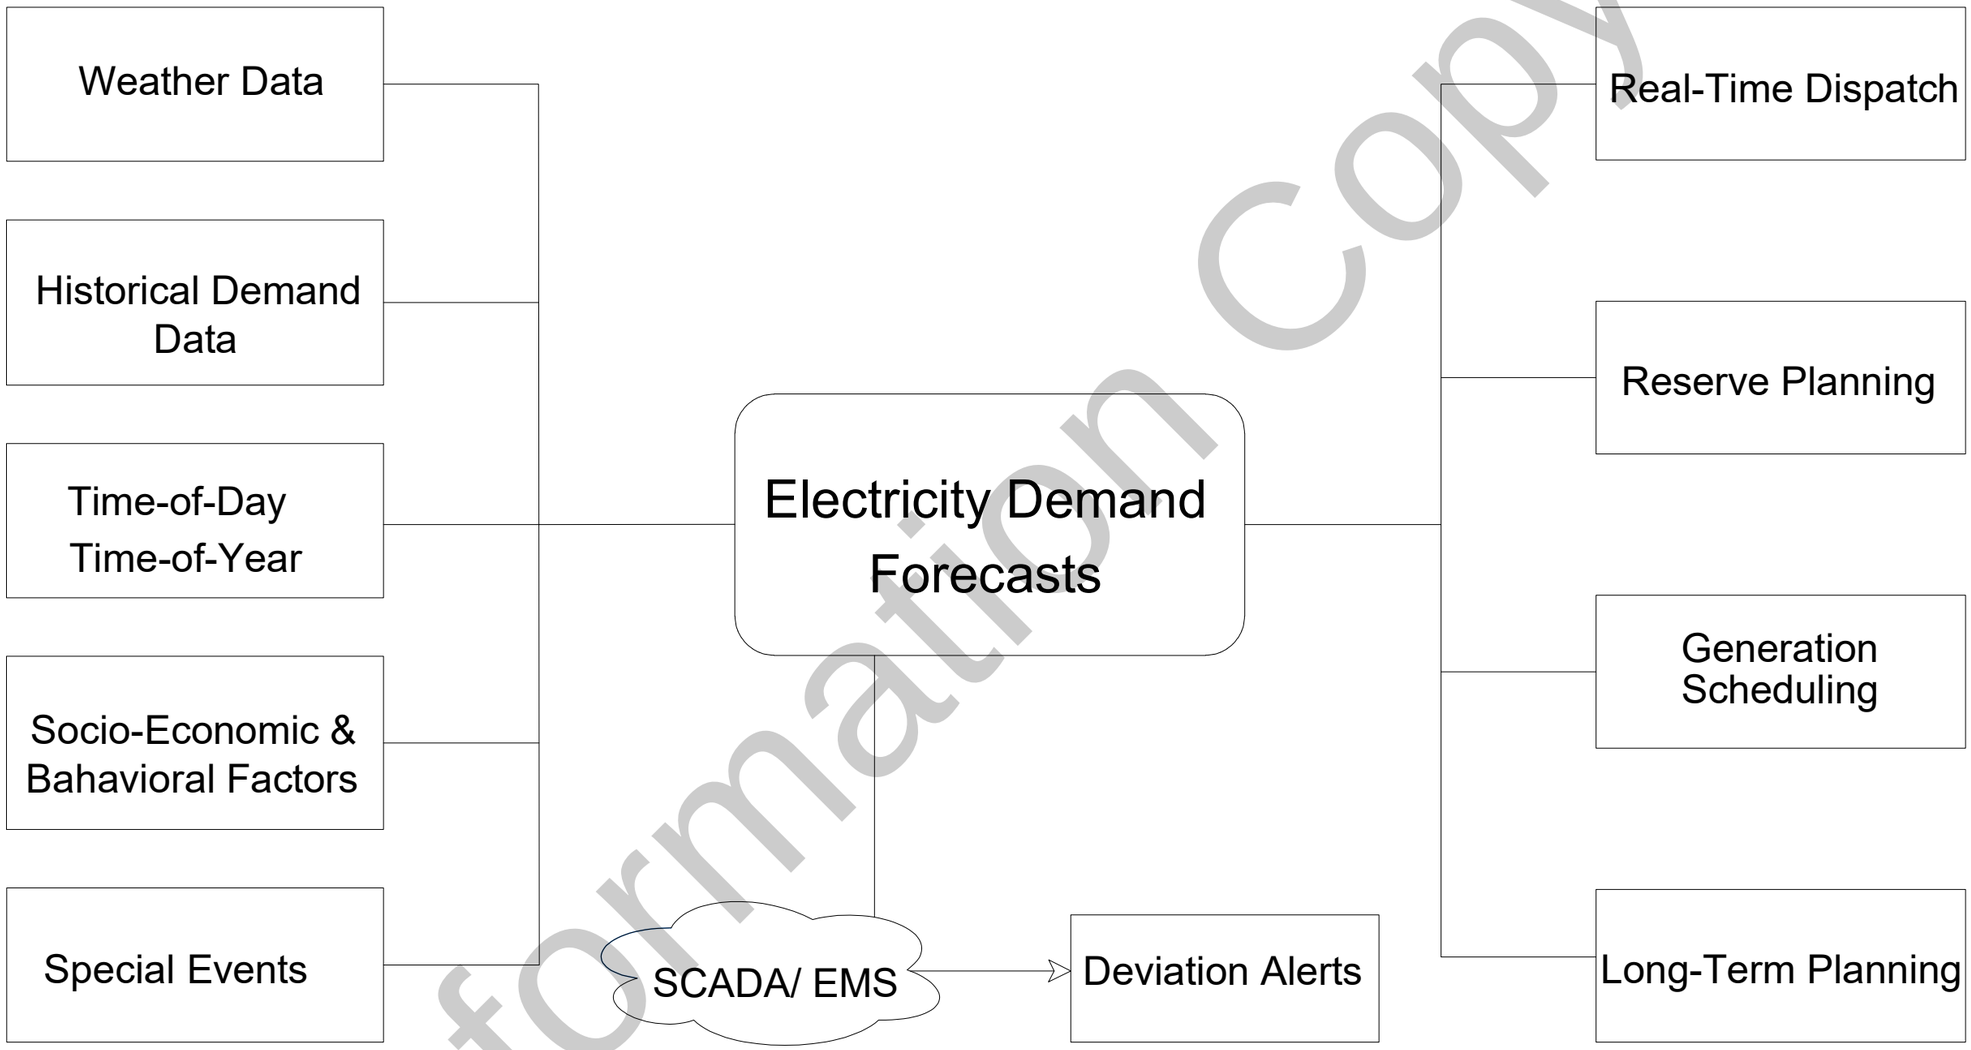

Minimum requirements are identified in the diagrams.

Information copy

Property of NTNSP Director Engineering

Property of NTNSP Director Engineering

Revision Record					
Rev. No.	Date	Description	Drawn	Checked	Approved

NTNSP NATIONAL TRANSMISSION NETWORK SERVICE PROVIDER (PRIVATE) LIMITED

NATIONAL TRANSMISSION NETWORK SERVICE PROVIDER (PVT) LTD
DIRECTOR ENGINEERING

Project Title
POWER SYSTEM STRENGTHENING AND RENEWABLE ENERGY INTEGRATION PROJECT (PSSREIP) PACKAGE 6

Funding Agency
ADB

Drawing Title
DEMAND FORECASTING SYSTEM (REMS)

Scale - NTS			Rev. Date		
Size - A3					
Sheet 01 of 01			Rev. 0		
Dwg. No. TD/CE/1/273/D/04					

		Signature	Date
Drawn	Sandamali		18.03.2026
Designed	Kasun		
Checked			
Approved			

Released for: Tendering ✓ / Construction

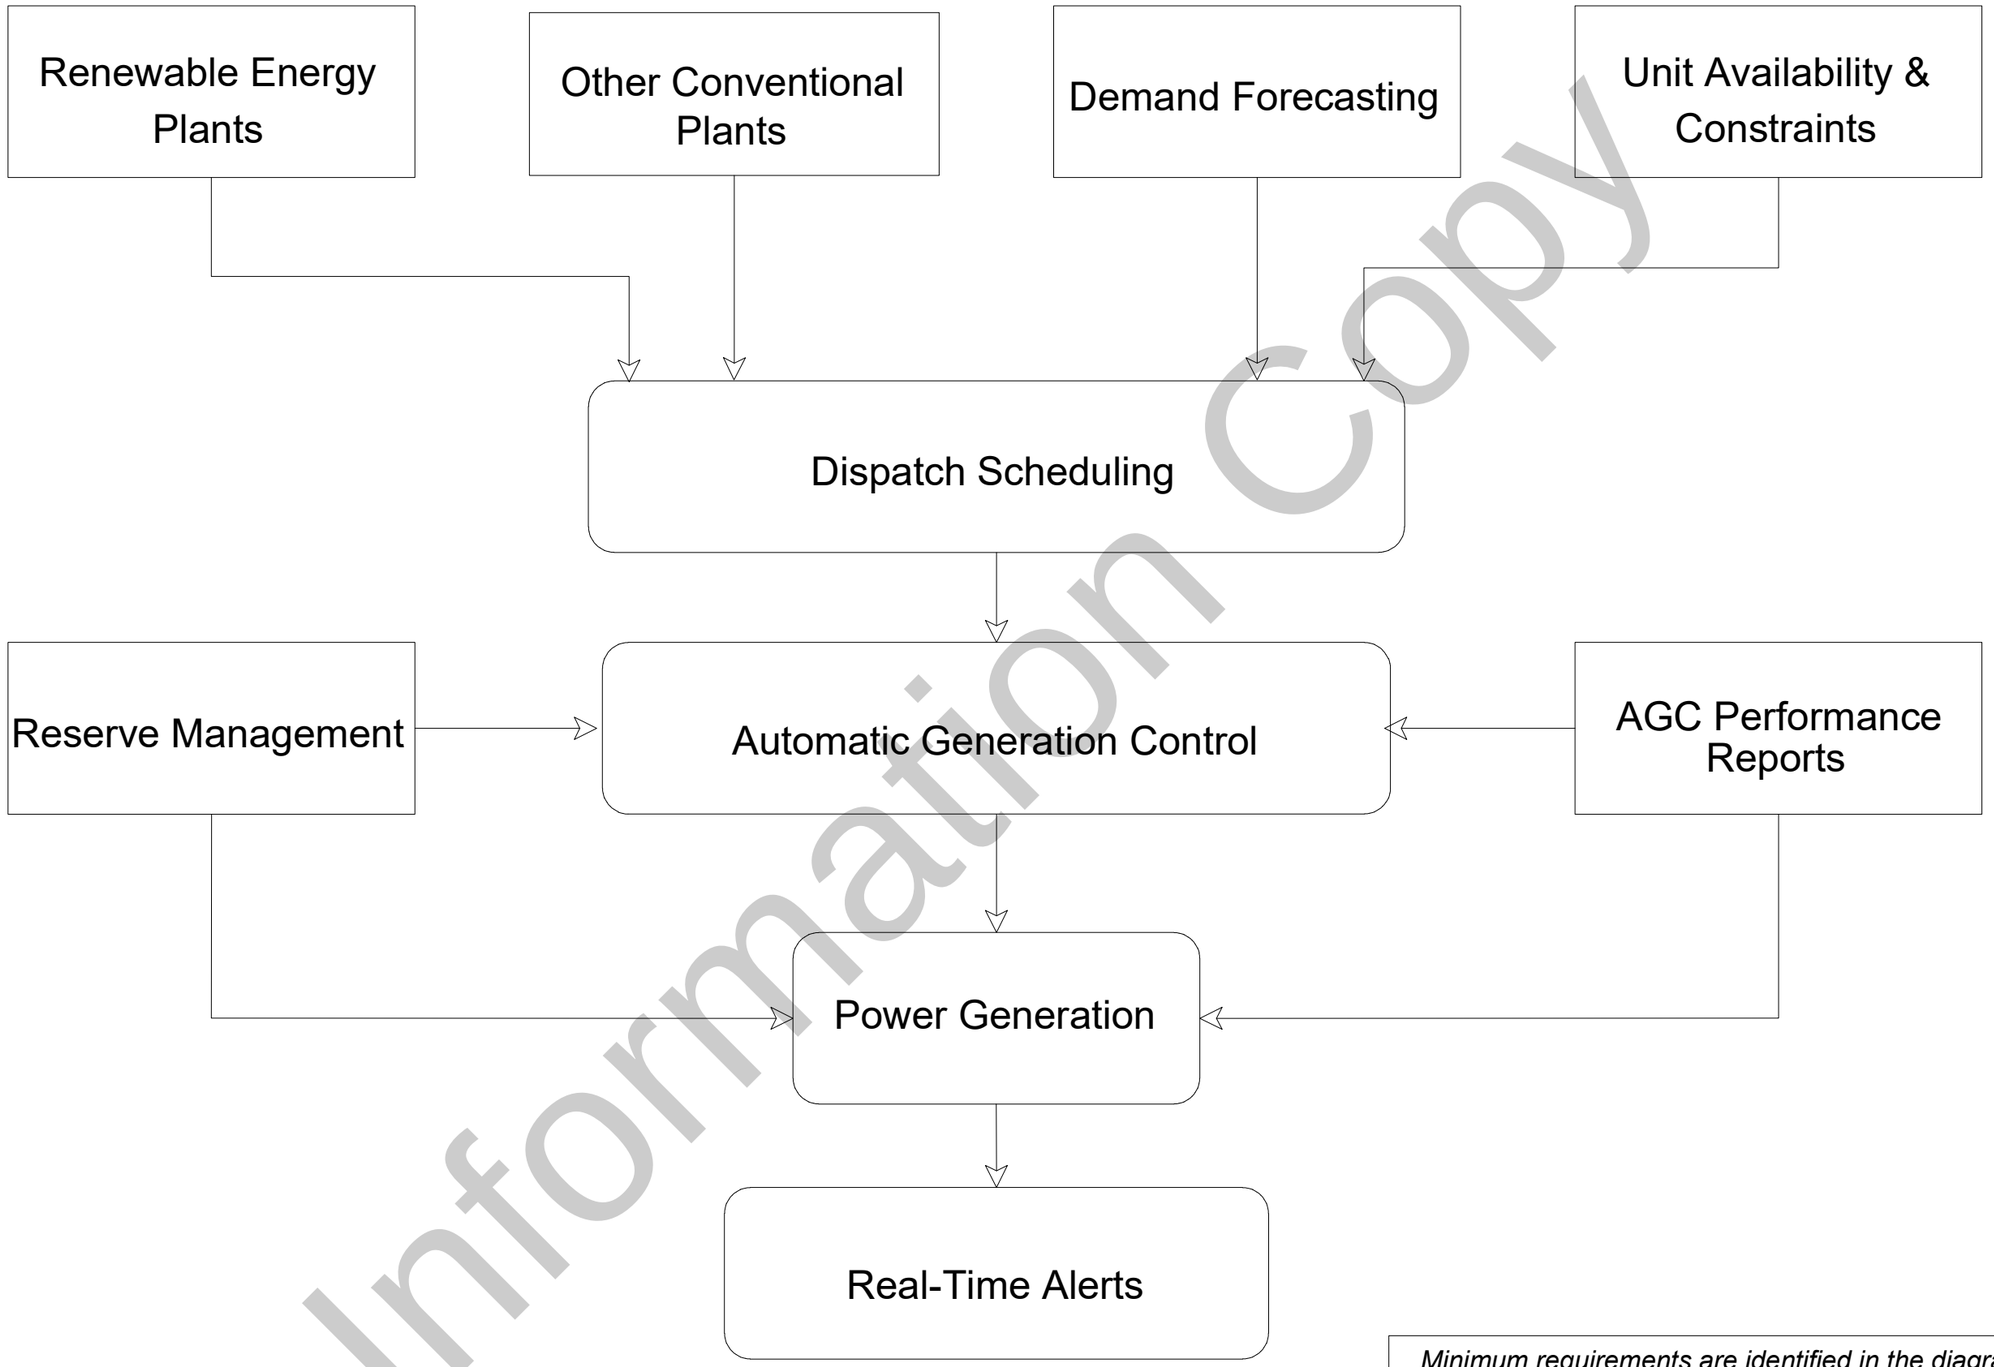

Minimum requirements are identified in the diagrams.

Information Copy

Property of NTNSP Director Engineering

Property of NTNSP Director Engineering

Revision Record					
Rev. No.	Date	Description	Drawn	Checked	Approved

NTNSP NATIONAL TRANSMISSION NETWORK SERVICE PROVIDER (PRIVATE) LIMITED

NATIONAL TRANSMISSION NETWORK SERVICE PROVIDER (PVT) LTD
DIRECTOR ENGINEERING

Project Title: ***POWER SYSTEM STRENGTHENING AND RENEWABLE ENERGY INTEGRATION PROJECT (PSSREIP) PACKAGE 6***

Funding Agency: ADB

Drawing Title: AUTOMATIC GENERATION CONTROL

Scale - NTS				Rev. Date		
Size - A3						
Sheet	01	of	01	Rev.	0	
Dwg. No. TD/CE/1/273/D/05						

		Signature	Date
Drawn	Sandamali		18.03.2026
Designed	Kasun		
Checked			
Approved			
Released for	Tendering		✓
	Construction		

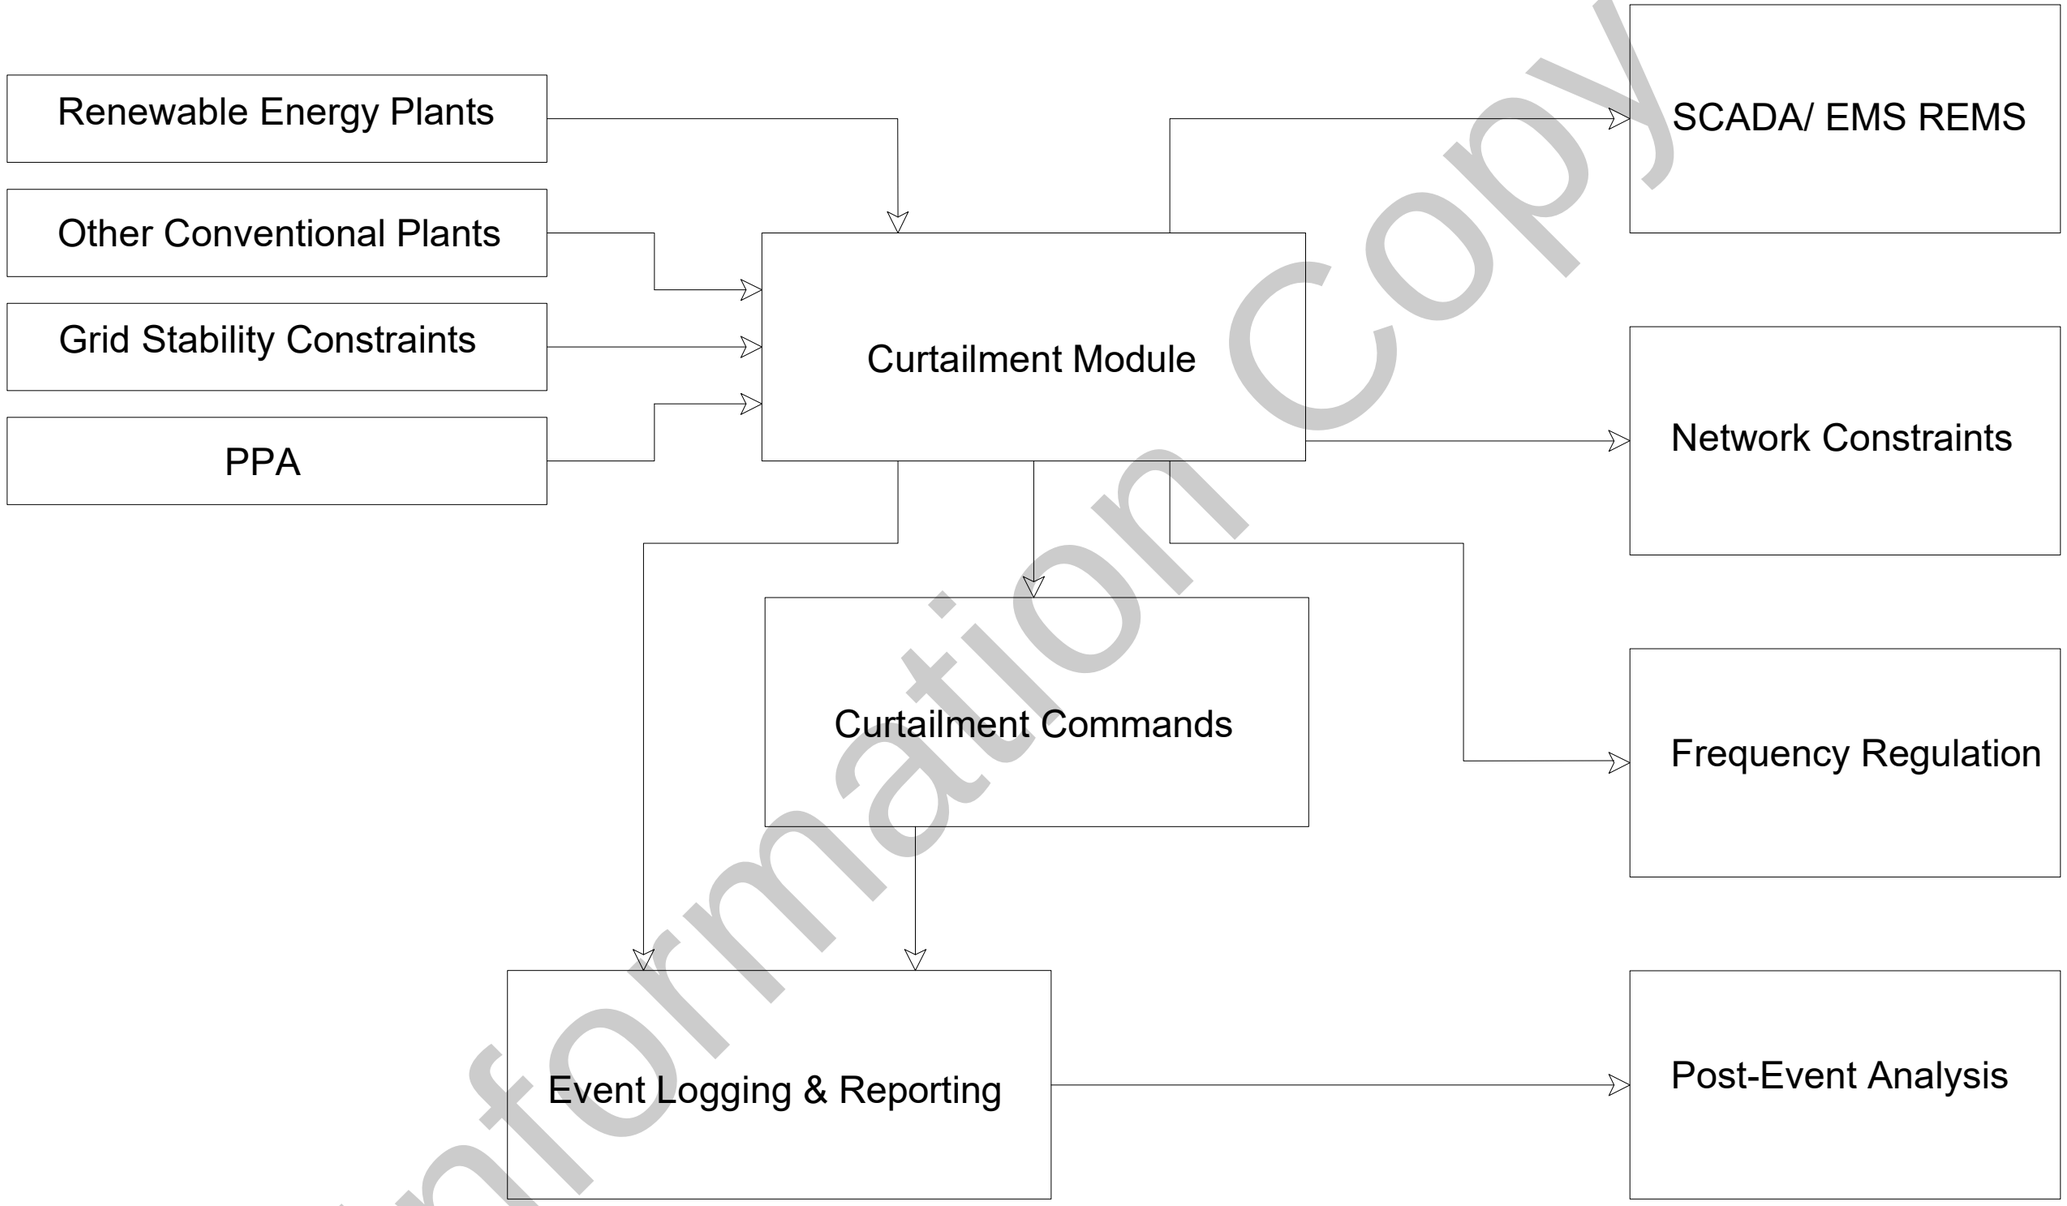

Minimum requirements are identified in the diagrams.

Information Copy

Property of NTNSP Director Engineering

Property of NTNSP Director Engineering

Revision Record					
Rev. No.	Date	Description	Drawn	Checked	Approved

NTNSP NATIONAL TRANSMISSION NETWORK SERVICE PROVIDER (PRIVATE) LIMITED

NATIONAL TRANSMISSION NETWORK SERVICE PROVIDER (PVT) LTD
DIRECTOR ENGINEERING

Project Title
POWER SYSTEM STRENGTHENING AND RENEWABLE ENERGY INTEGRATION PROJECT (PSSREIP) PACKAGE 6

Funding Agency
ADB

Drawing Title
TRANSPARENT GENERATION MANAGEMENT & CURTAILMENT SYSTEM

Scale - NTS			Rev. Date		
Size - A3					
Sheet 01 of 01			Rev. 0		
Dwg. No. TD/CE/1/273/D/06					

		Signature	Date
Drawn	Sandamali		18.03.2026
Designed	Kasun		
Checked			
Approved			
Released for	Tendering		✓
	Construction		

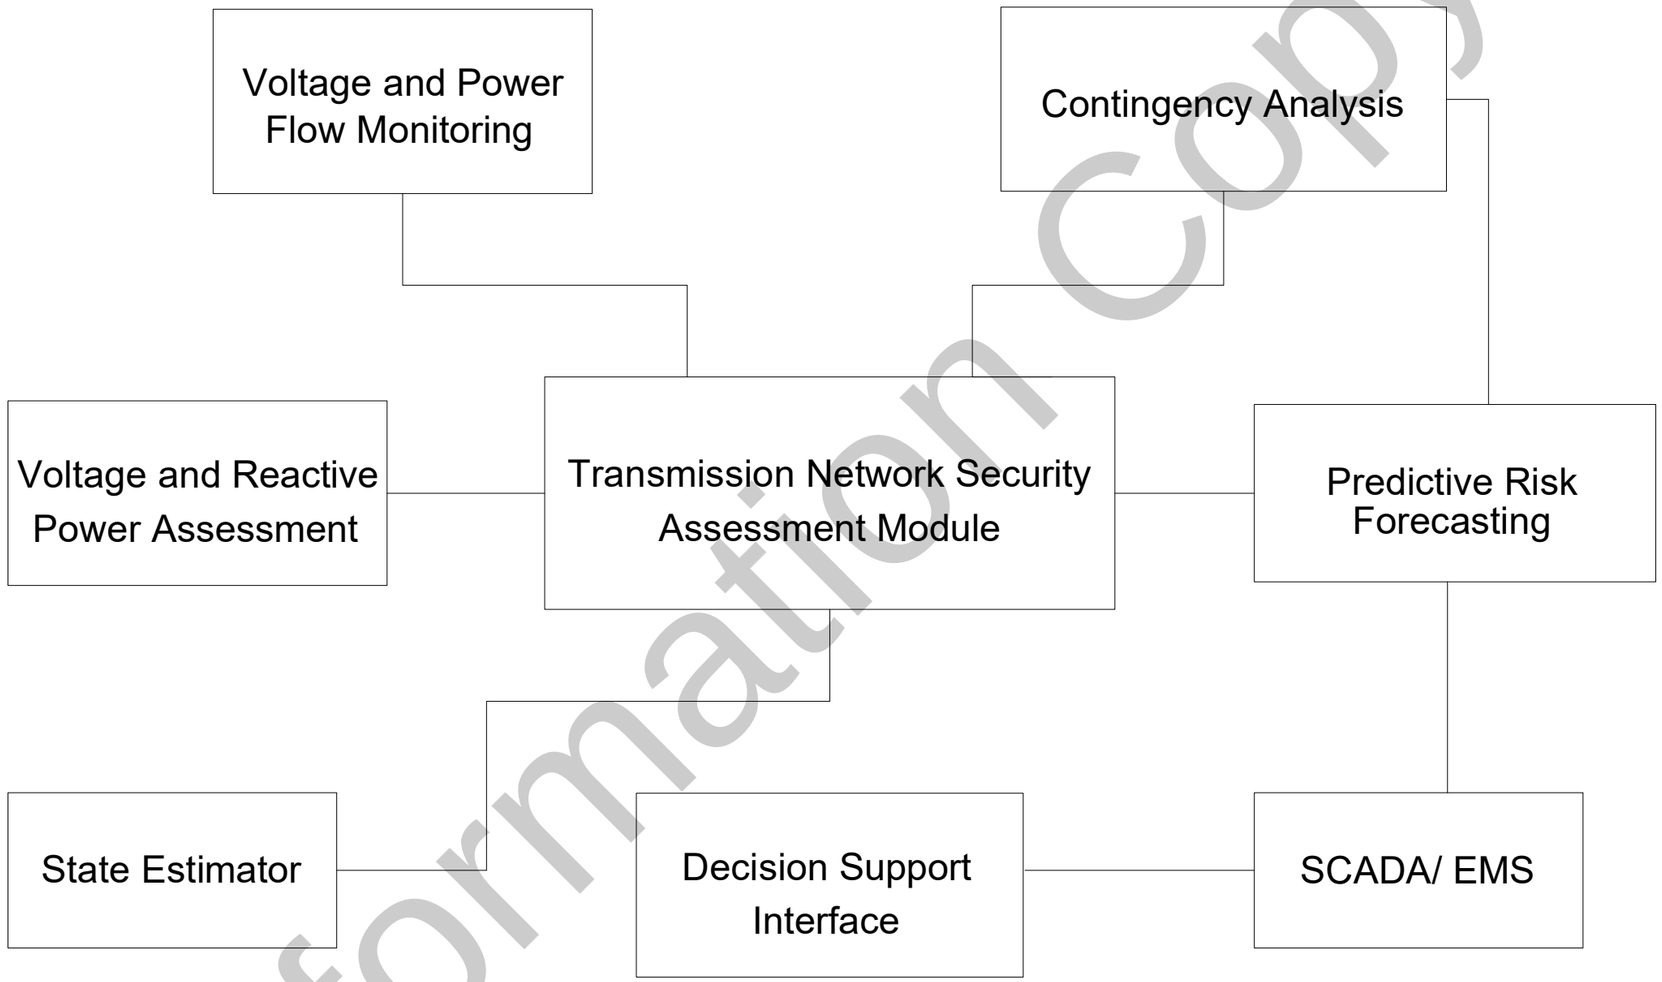

Minimum requirements are identified in the diagrams.

Information Copy

Property of NTNSP Director Engineering

Property of NTNSP Director Engineering

Revision Record					
Rev. No.	Date	Description	Drawn	Checked	Approved

NTNSP NATIONAL TRANSMISSION NETWORK SERVICE PROVIDER (PRIVATE) LIMITED

NATIONAL TRANSMISSION NETWORK SERVICE PROVIDER (PVT) LTD
DIRECTOR ENGINEERING

Project Title
POWER SYSTEM STRENGTHENING AND RENEWABLE ENERGY INTEGRATION PROJECT (PSSREIP) PACKAGE 6

Funding Agency
ADB

Drawing Title
TRANSMISSION NETWORK SECURITY ASSESSMENT

Scale -	NTS		Rev. Date		
Size -	A3				
Sheet	01 of 01		Rev.	0	
Dwg. No.	TD/CE/1/273/D/07				

		Signature	Date
Drawn	Sandamali		18.03.2026
Designed	Kasun		
Checked			
Approved			
Released for	Tendering		✓
	Construction		

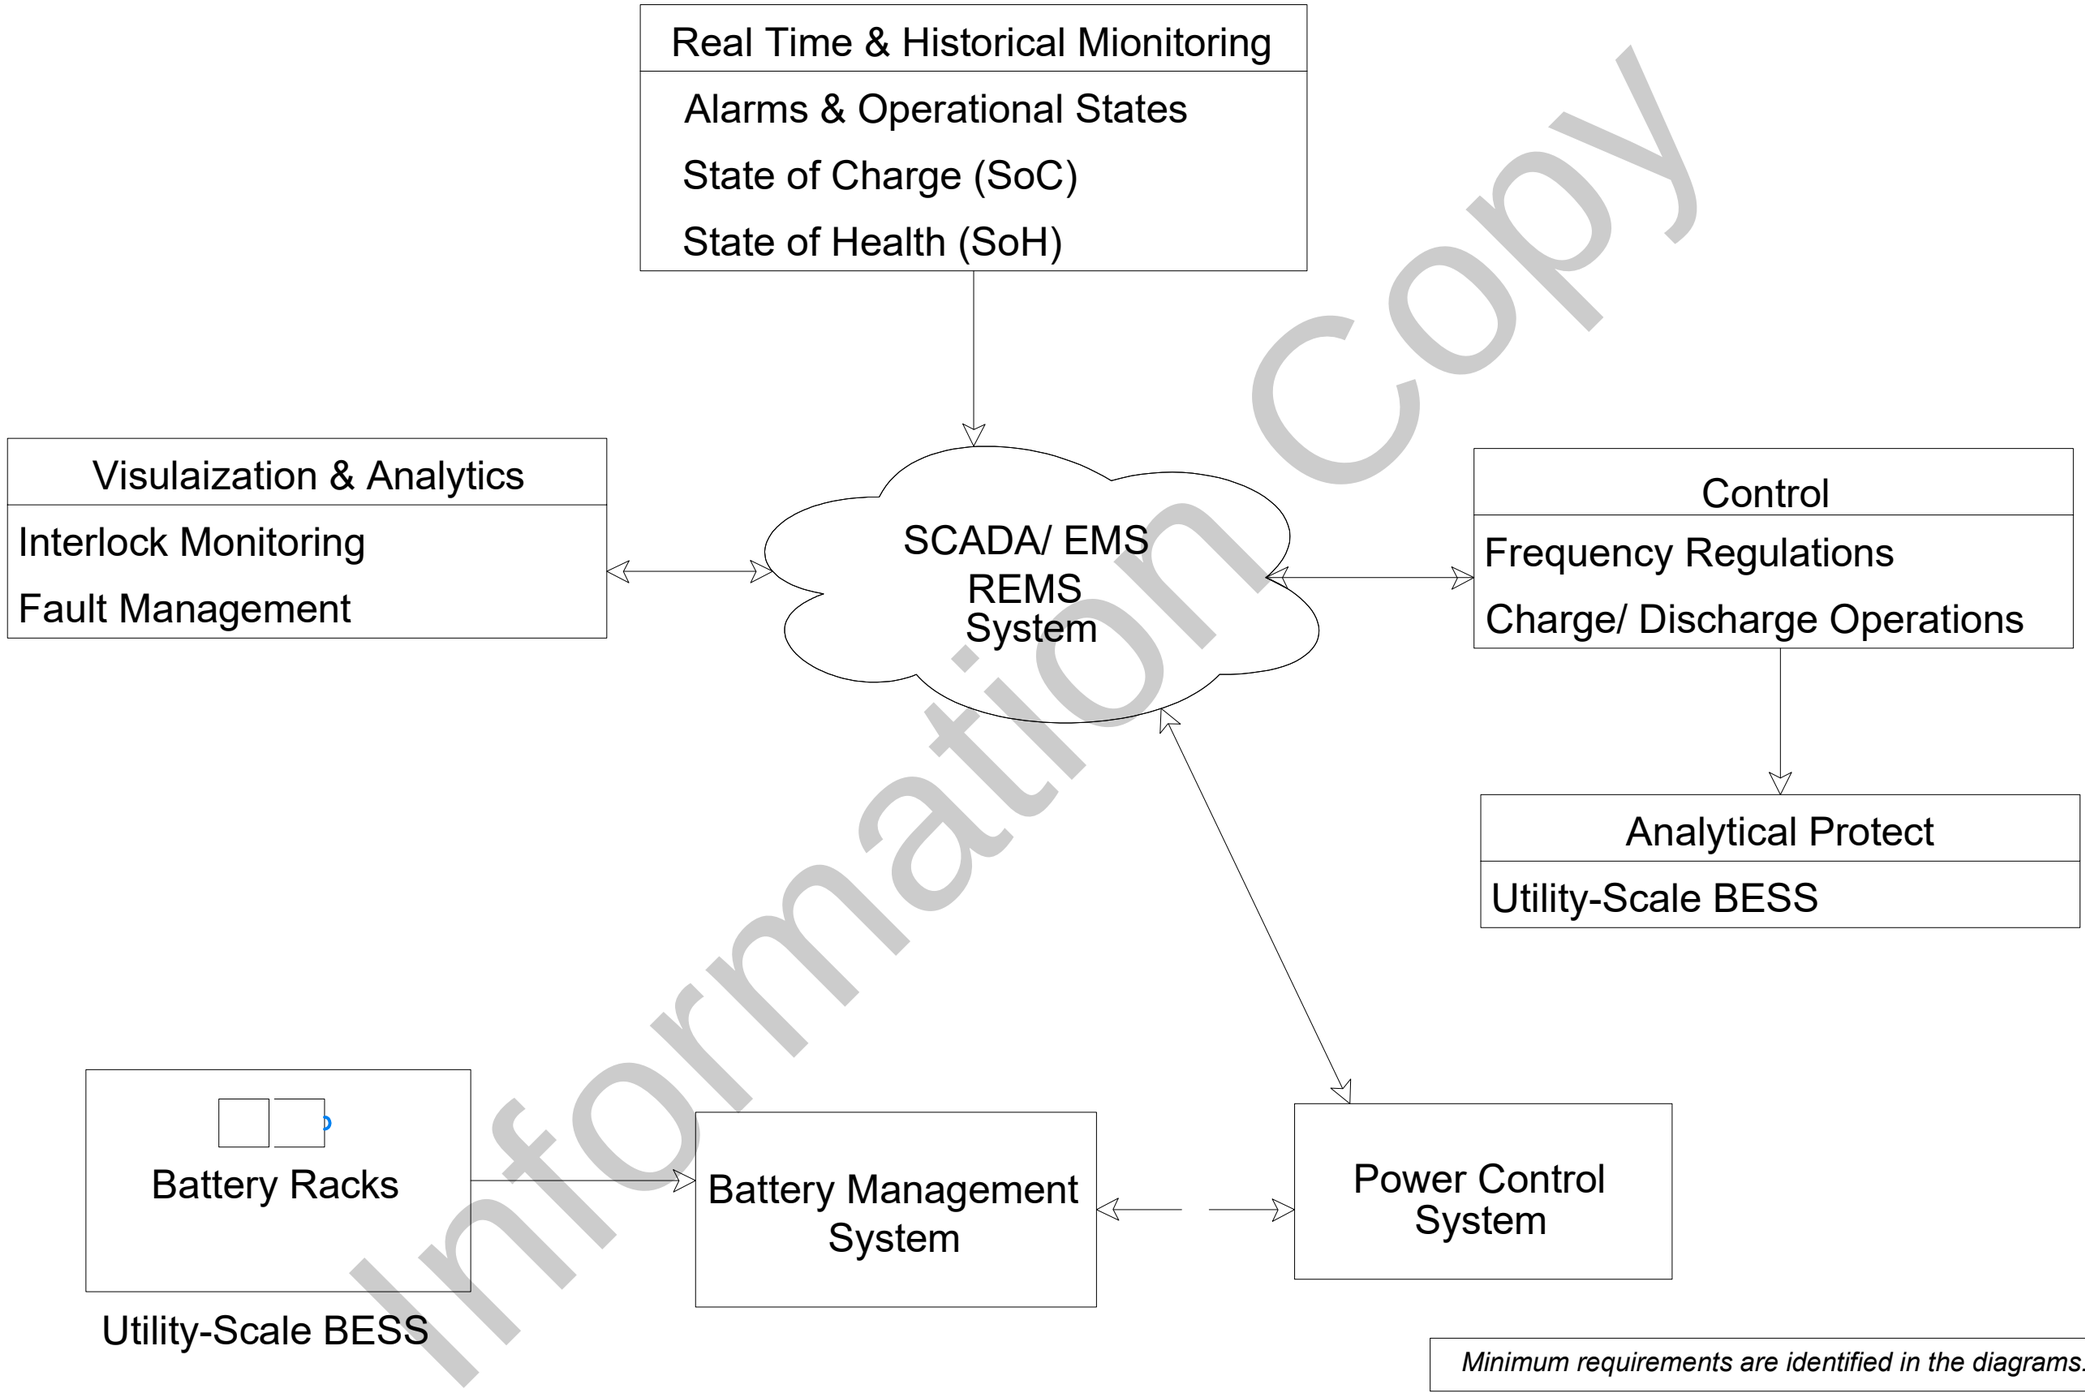

Information copy

Property of NTNSP Director Engineering

Property of NTNSP Director Engineering

Revision Record					
Rev. No.	Date	Description	Drawn	Checked	Approved

NTNSP NATIONAL TRANSMISSION NETWORK SERVICE PROVIDER (PRIVATE) LIMITED

NATIONAL TRANSMISSION NETWORK SERVICE PROVIDER (PVT) LTD
DIRECTOR ENGINEERING

Project Title
POWER SYSTEM STRENGTHENING AND RENEWABLE ENERGY INTEGRATION PROJECT (PSSREIP) PACKAGE 6

Funding Agency
ADB

Drawing Title
BATTERY ENERGY STORAGE SYSTEM
MONITORING & CONTROLING

Scale -	NTS		Rev. Date		
Size -	A3				
Sheet	01 of 01		Rev.	0	
Dwg. No.	TD/CE/1/273/D/08				

		Signature	Date
Drawn	Sandamali		18.03.2026
Designed	Kasun		
Checked			
Approved			
Released for	Tendering		✓
	Construction		

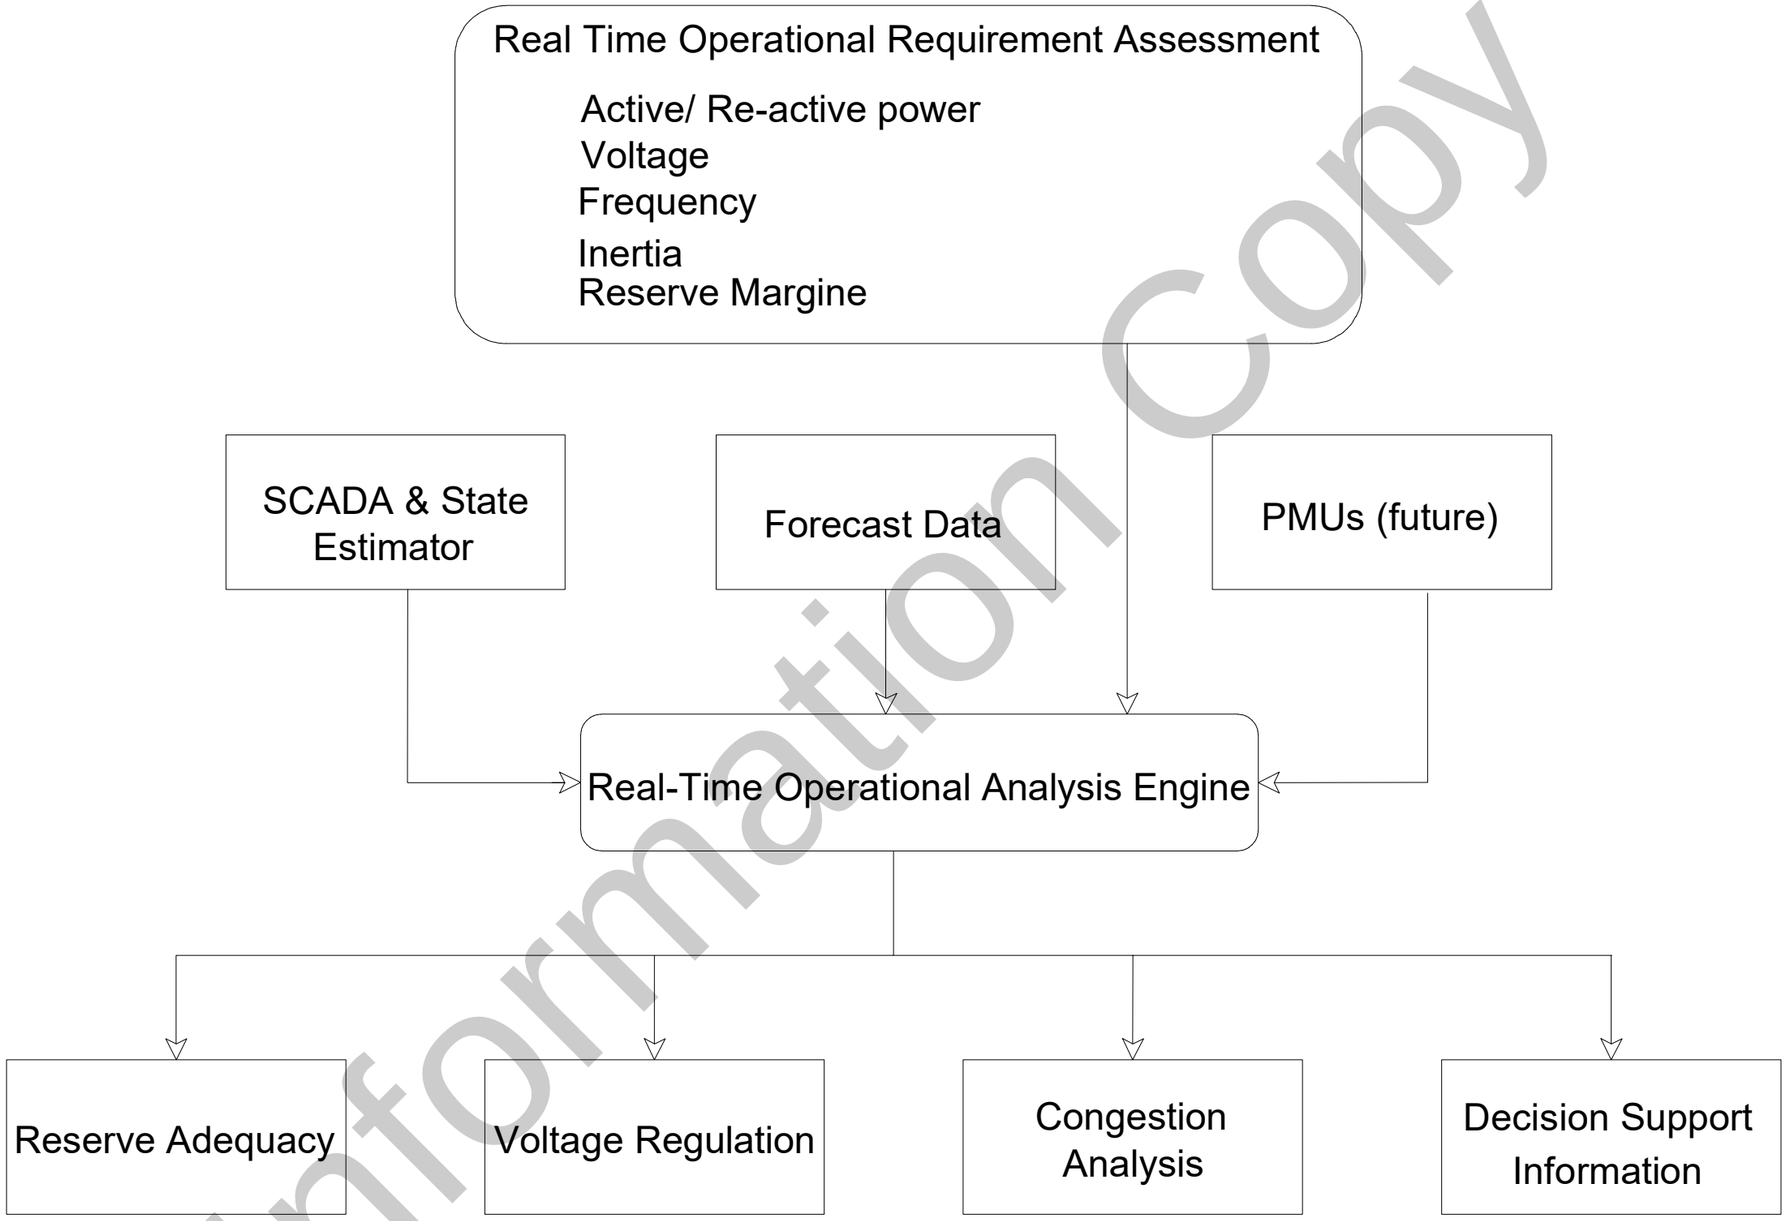

Minimum requirements are identified in the diagrams.

Information Copy

Property of NTNSP Director Engineering

Revision Record					
Rev. No.	Date	Description	Drawn	Checked	Approved

NTNSP NATIONAL TRANSMISSION NETWORK SERVICE PROVIDER (PRIVATE) LIMITED

NATIONAL TRANSMISSION NETWORK SERVICE PROVIDER (PVT) LTD
DIRECTOR ENGINEERING

Project Title: ***POWER SYSTEM STRENGTHENING AND RENEWABLE ENERGY INTEGRATION PROJECT (PSSREIP) PACKAGE 6***

Funding Agency: ADB

Drawing Title: REAL TIME OPERATIONAL REQUIREMENT ASSESSMENT

Scale - NTS			Rev. Date		
Size - A3					
Sheet	01 of 01		Rev.	0	
Dwg. No. TD/CE/1/273/D/09					

		Signature	Date
Drawn	Sandamali		18.03.2026
Designed	Kasun		
Checked			
Approved			
Released for	Tendering		✓
	Construction		

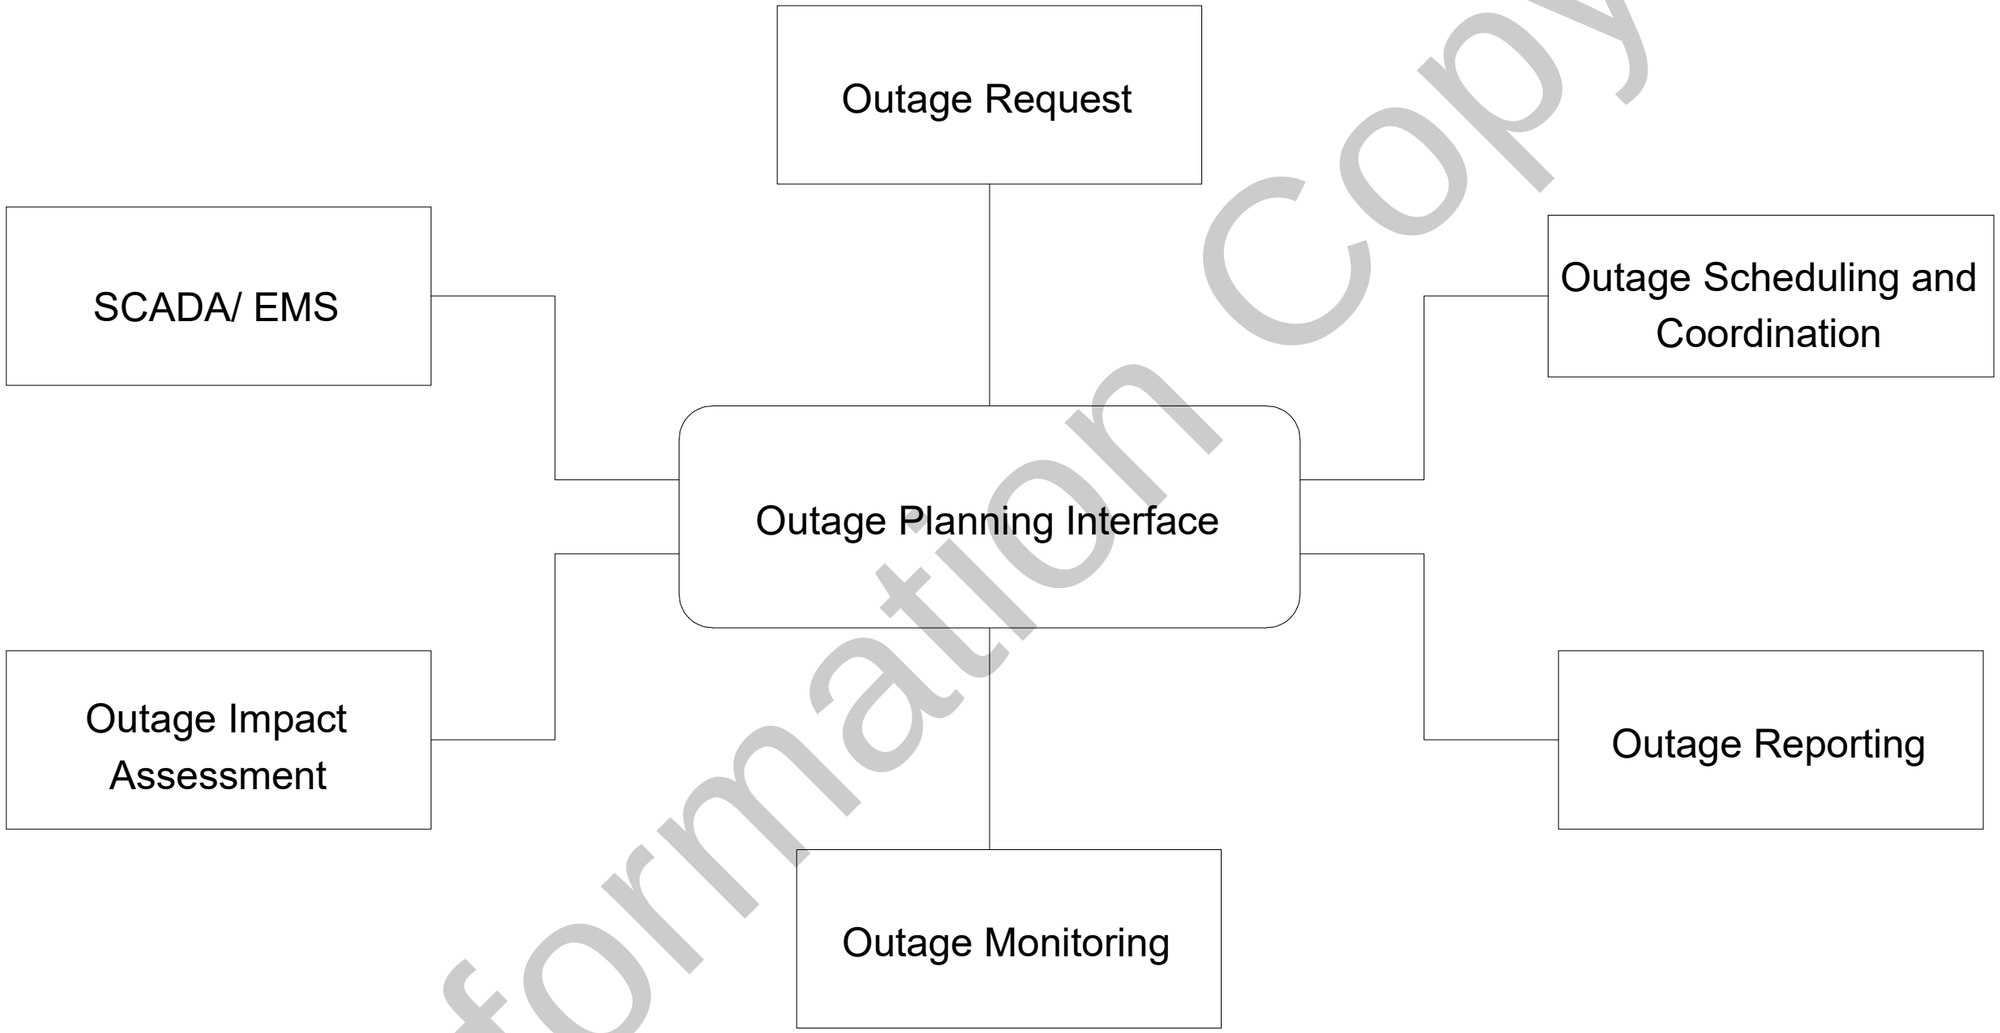

Minimum requirements are identified in the diagrams.

Information Copy

Property of NTNSP Director Engineering

Property of NTNSP Director Engineering

Revision Record					
Rev. No.	Date	Description	Drawn	Checked	Approved

NTNSP NATIONAL TRANSMISSION NETWORK SERVICE PROVIDER (PRIVATE) LIMITED

NATIONAL TRANSMISSION NETWORK SERVICE PROVIDER (PVT) LTD
DIRECTOR ENGINEERING

Project Title
POWER SYSTEM STRENGTHENING AND RENEWABLE ENERGY INTEGRATION PROJECT (PSSREIP) PACKAGE 6

Funding Agency
ADB

Drawing Title
OUTAGE PLANING INTERFACE

Scale -	NTS	Rev. Date	
Size -	A3		
Sheet	01 of 01	Rev.	0
Dwg. No.	TD/CE/1/273/D/10		

		Signature	Date
Drawn	Sandamali		18.03.2026
Designed	Kasun		
Checked			
Approved			

Released for		
	Tendering	✓
	Construction	

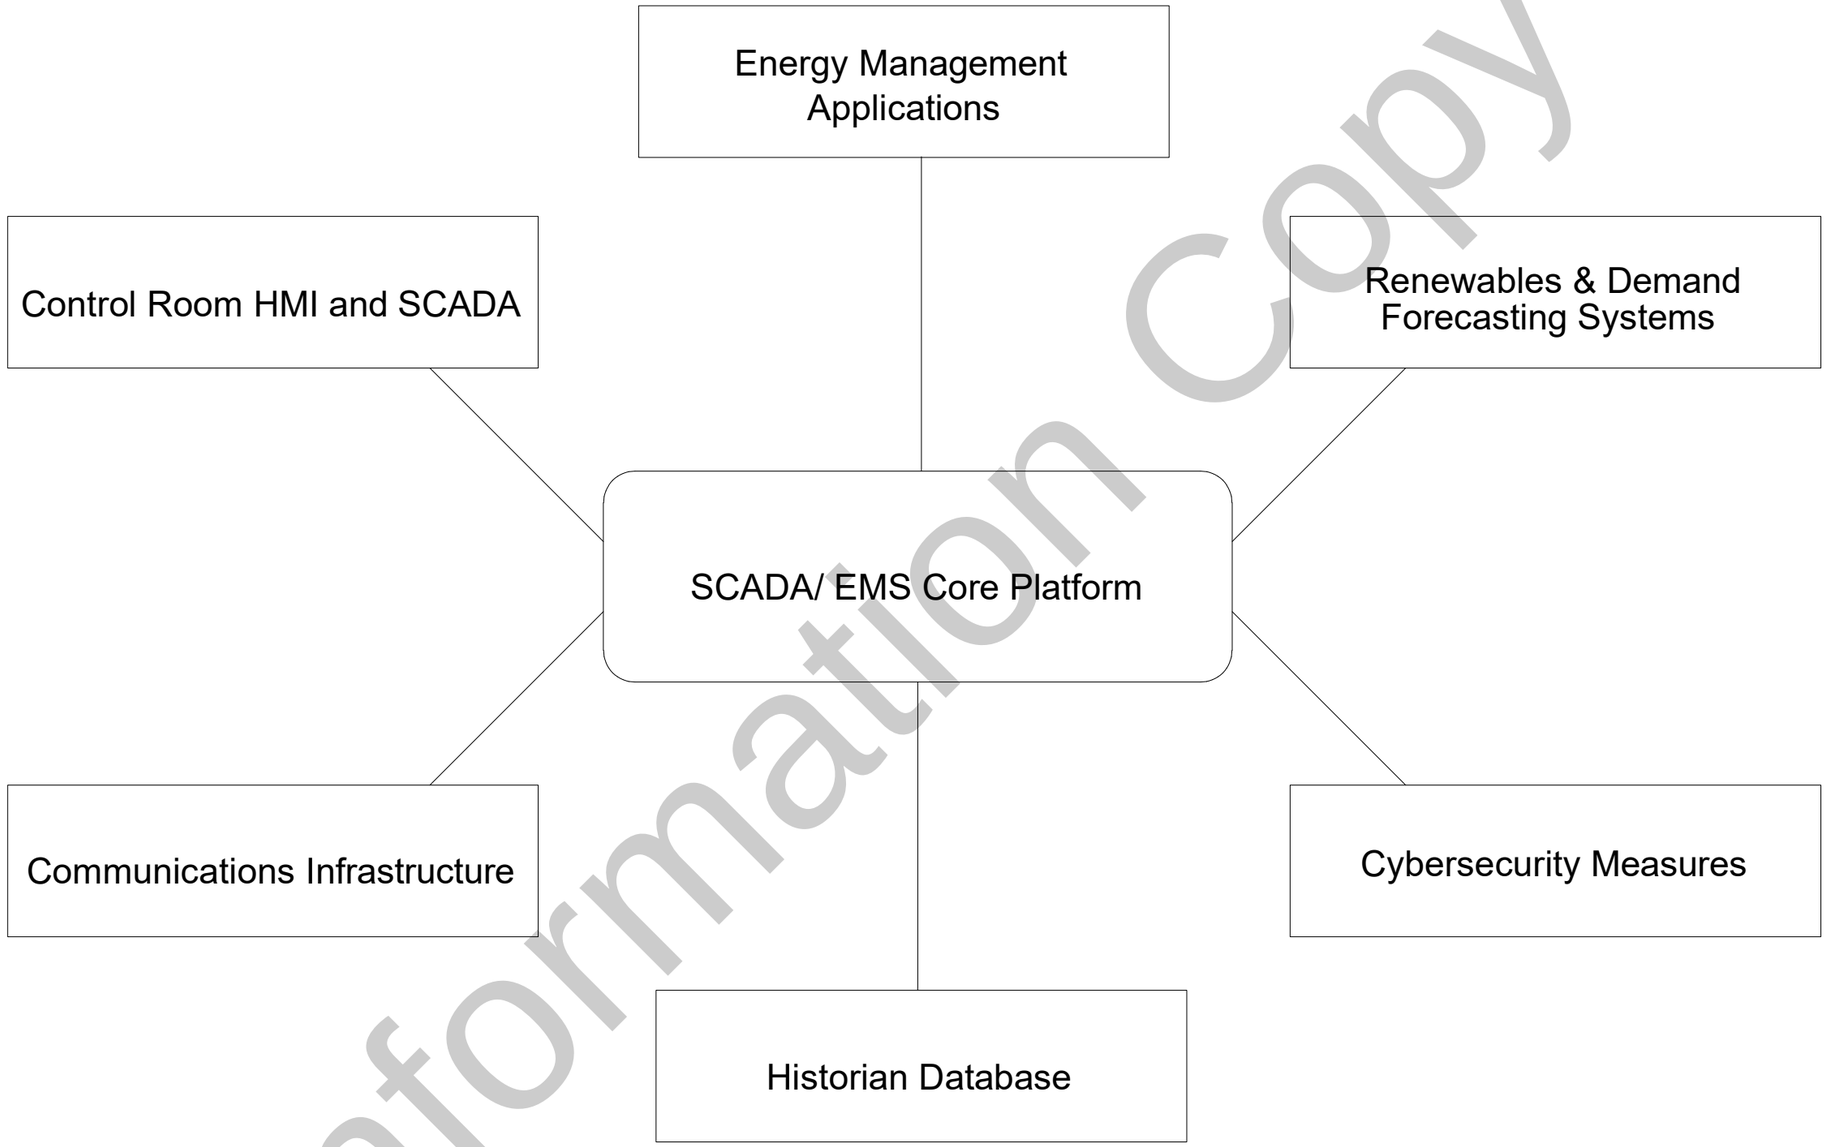

Minimum requirements are identified in the diagrams.

Information Copy

Property of NTNSP Director Engineering

Property of NTNSP Director Engineering

Revision Record					
Rev. No.	Date	Description	Drawn	Checked	Approved

NTNSP NATIONAL TRANSMISSION NETWORK SERVICE PROVIDER (PRIVATE) LIMITED

NATIONAL TRANSMISSION NETWORK SERVICE PROVIDER (PVT) LTD
DIRECTOR ENGINEERING

Project Title
POWER SYSTEM STRENGTHENING AND RENEWABLE ENERGY INTEGRATION PROJECT (PSSREIP) PACKAGE 6

Funding Agency
ADB

Drawing Title
OUTAGE PLANING INTERFACE

Scale - NTS			Rev. Date		
Size - A3					
Sheet 01 of 01	Rev. 0				
Dwg. No. TD/CE/1/273/D/11					

		Signature	Date
Drawn	Sandamali		18.03.2026
Designed	Kasun		
Checked			
Approved			
Released for	Tendering		✓
	Construction		

SCADA/ EMS	REMS	AGC

Control Centre Operational Display

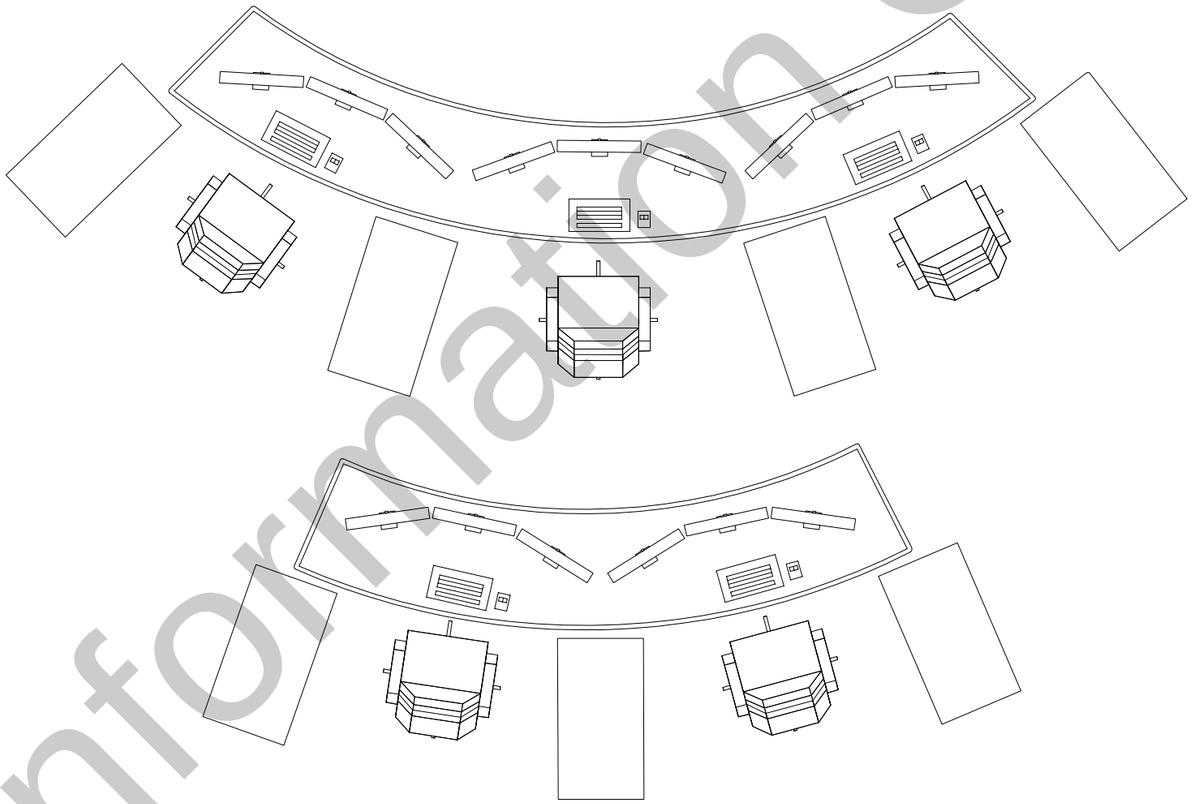

NOTE -

** FLOOR WOODEN*
** RAISED FLOOR FOR BACK TABLE*

Minimum requirements are identified in the diagrams.

Information Copy

Property of NTNSP Director Engineering

Property of NTNSP Director Engineering

Revision Record

Rev. No.	Date	Description	Drawn	Checked	Approved

NTNSP NATIONAL TRANSMISSION NETWORK SERVICE PROVIDER (PRIVATE) LIMITED

NATIONAL TRANSMISSION NETWORK SERVICE PROVIDER (PVT) LTD
DIRECTOR ENGINEERING

Project Title
POWER SYSTEM STRENGTHENING AND RENEWABLE ENERGY INTEGRATION PROJECT (PSSREIP) PACKAGE 6

Funding Agency
ADB

Drawing Title
CONTROL CENTER OPERATIONAL DISPLAY AND INFRASTRUCTURE

Scale - NTS
Size - A3
Sheet 01 of 01 Rev. 0
Dwg. No. TD/CE/1/273/D/12

Rev. Date		Signature	Date
	Drawn	Sandamali	18.03.2026
	Designed	Kasun	
	Checked		
	Approved		

Released for: Tendering ✓ ; Construction

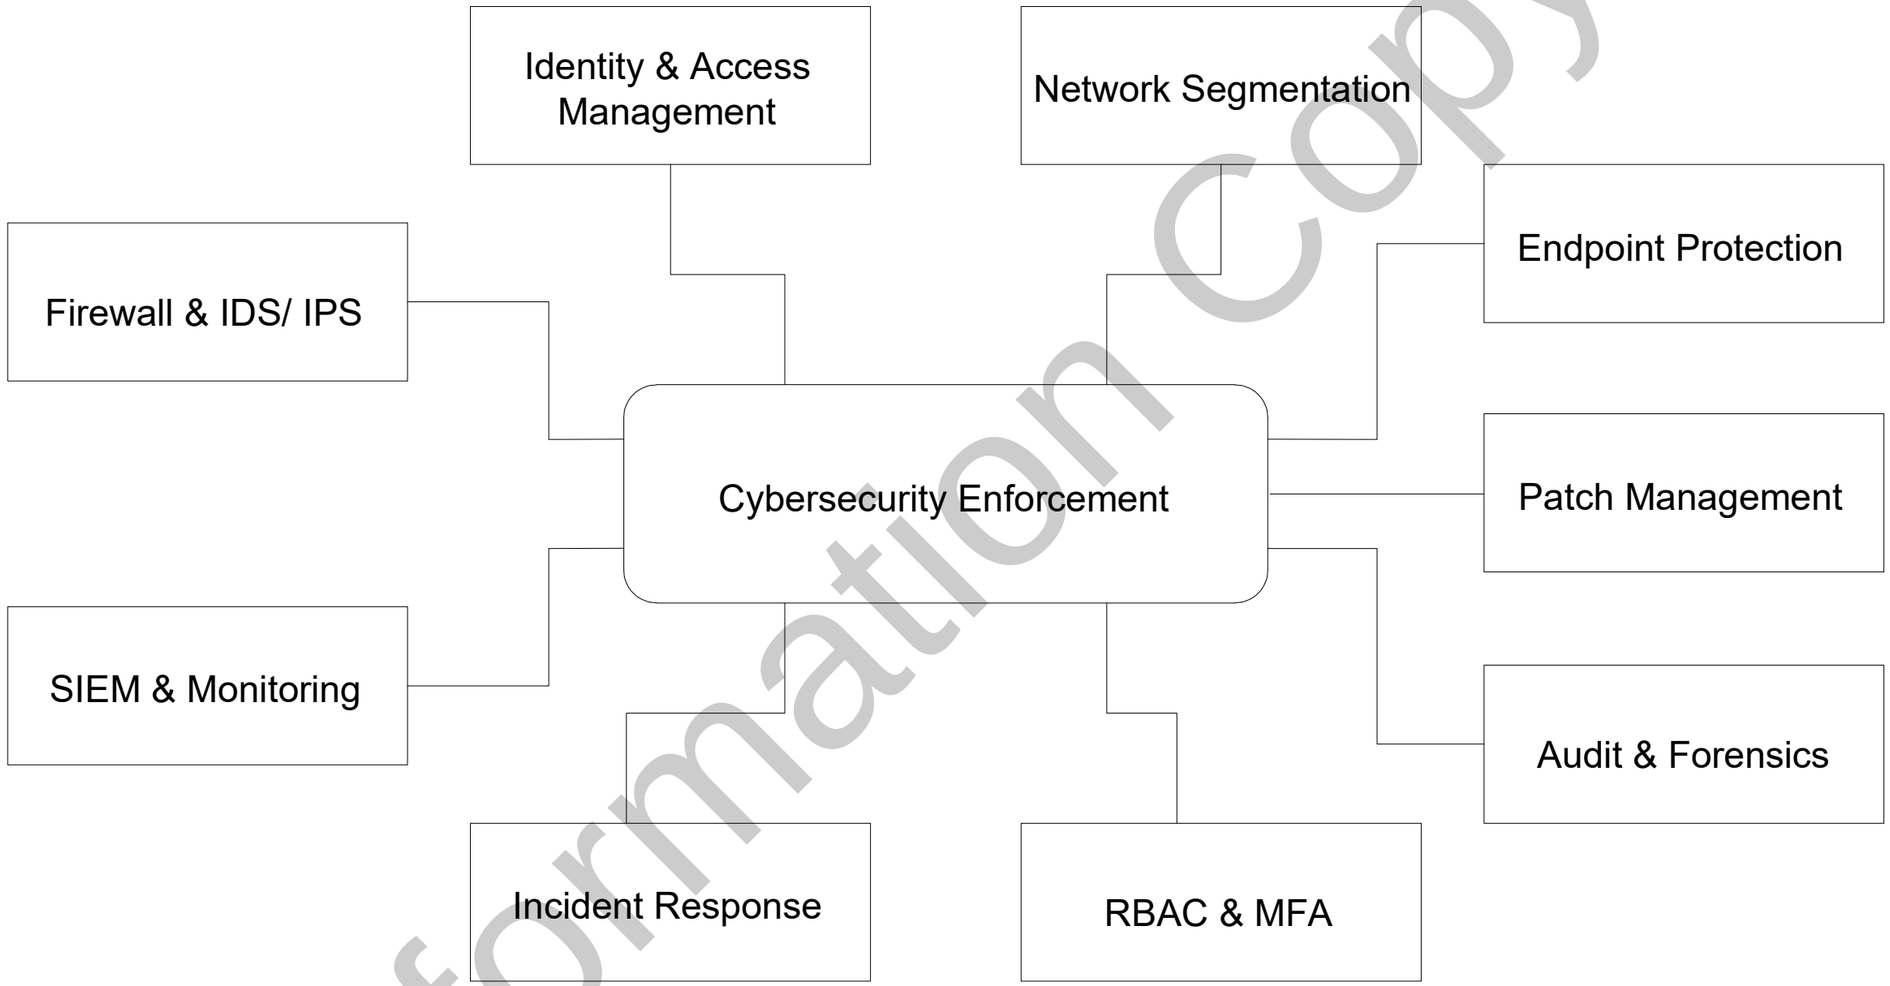

Minimum requirements are identified in the diagrams.

Information Copy

Property of NTNSP Director Engineering

Property of NTNSP Director Engineering

Revision Record					
Rev. No.	Date	Description	Drawn	Checked	Approved

NTNSP NATIONAL TRANSMISSION NETWORK SERVICE PROVIDER (PRIVATE) LIMITED

NATIONAL TRANSMISSION NETWORK SERVICE PROVIDER (PVT) LTD
DIRECTOR ENGINEERING

Project Title
POWER SYSTEM STRENGTHENING AND RENEWABLE ENERGY INTEGRATION PROJECT (PSSREIP) PACKAGE 6

Funding Agency
ADB

Drawing Title
IMPLEMENTATION OF CYBERSECURITY ENFORCEMENT

Scale - NTS			Rev. Date		
Size - A3					
Sheet 01 of 01			Rev. 0		
Dwg. No. TD/CE/1/273/D/13					

		Signature	Date
Drawn	Sandamali		18.03.2026
Designed	Kasun		
Checked			
Approved			
Released for	Tendering		✓
	Construction		

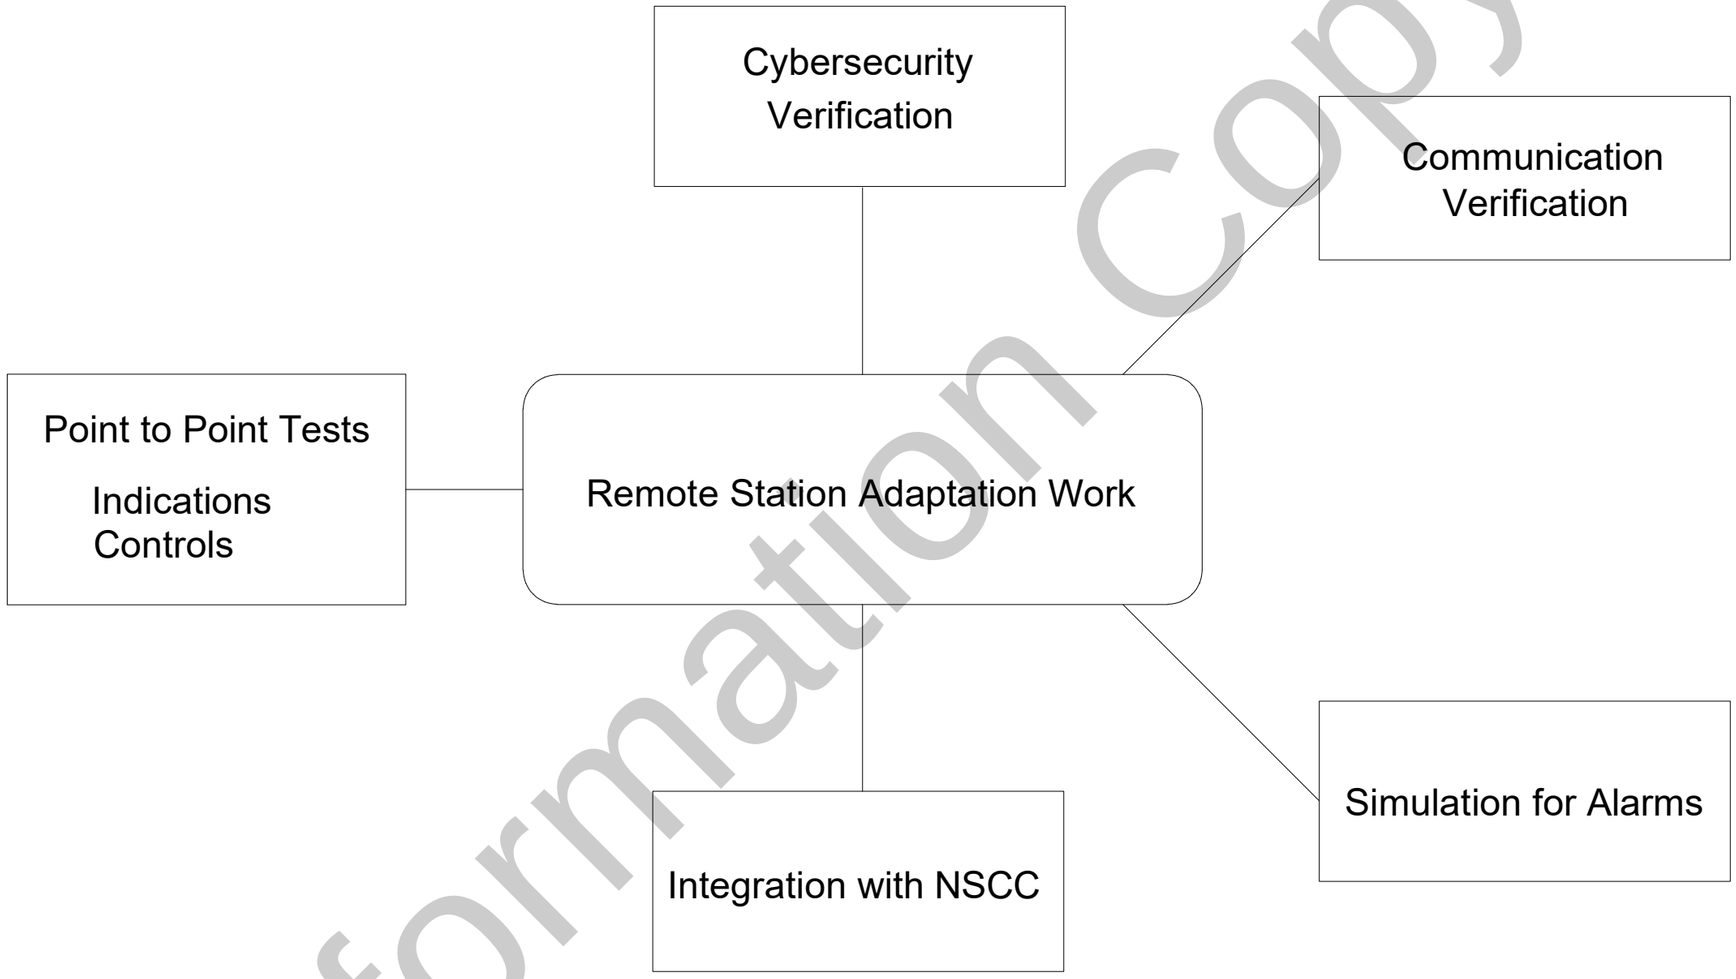

Minimum requirements are identified in the diagrams.

Information Copy

Property of NTNSP Director Engineering

Revision Record					
Rev. No.	Date	Description	Drawn	Checked	Approved

NTNSP NATIONAL TRANSMISSION NETWORK SERVICE PROVIDER (PRIVATE) LIMITED

NATIONAL TRANSMISSION NETWORK SERVICE PROVIDER (PVT) LTD
DIRECTOR ENGINEERING

Project Title: ***POWER SYSTEM STRENGTHENING AND RENEWABLE ENERGY INTEGRATION PROJECT (PSSREIP) PACKAGE 6***

Funding Agency: ADB

Drawing Title: REMOTE STATIO ADAPTATION WORK

Scale - NTS	Rev. Date		
Size - A3			
Sheet 01 of 01	Rev. 0		
Dwg. No. TD/CE/1/273/D/14			

	Signature		Date
Drawn	Sandamali		18.03.2026
Designed	Kasun		
Checked			
Approved			

Released for: Tendering ✓ ; Construction

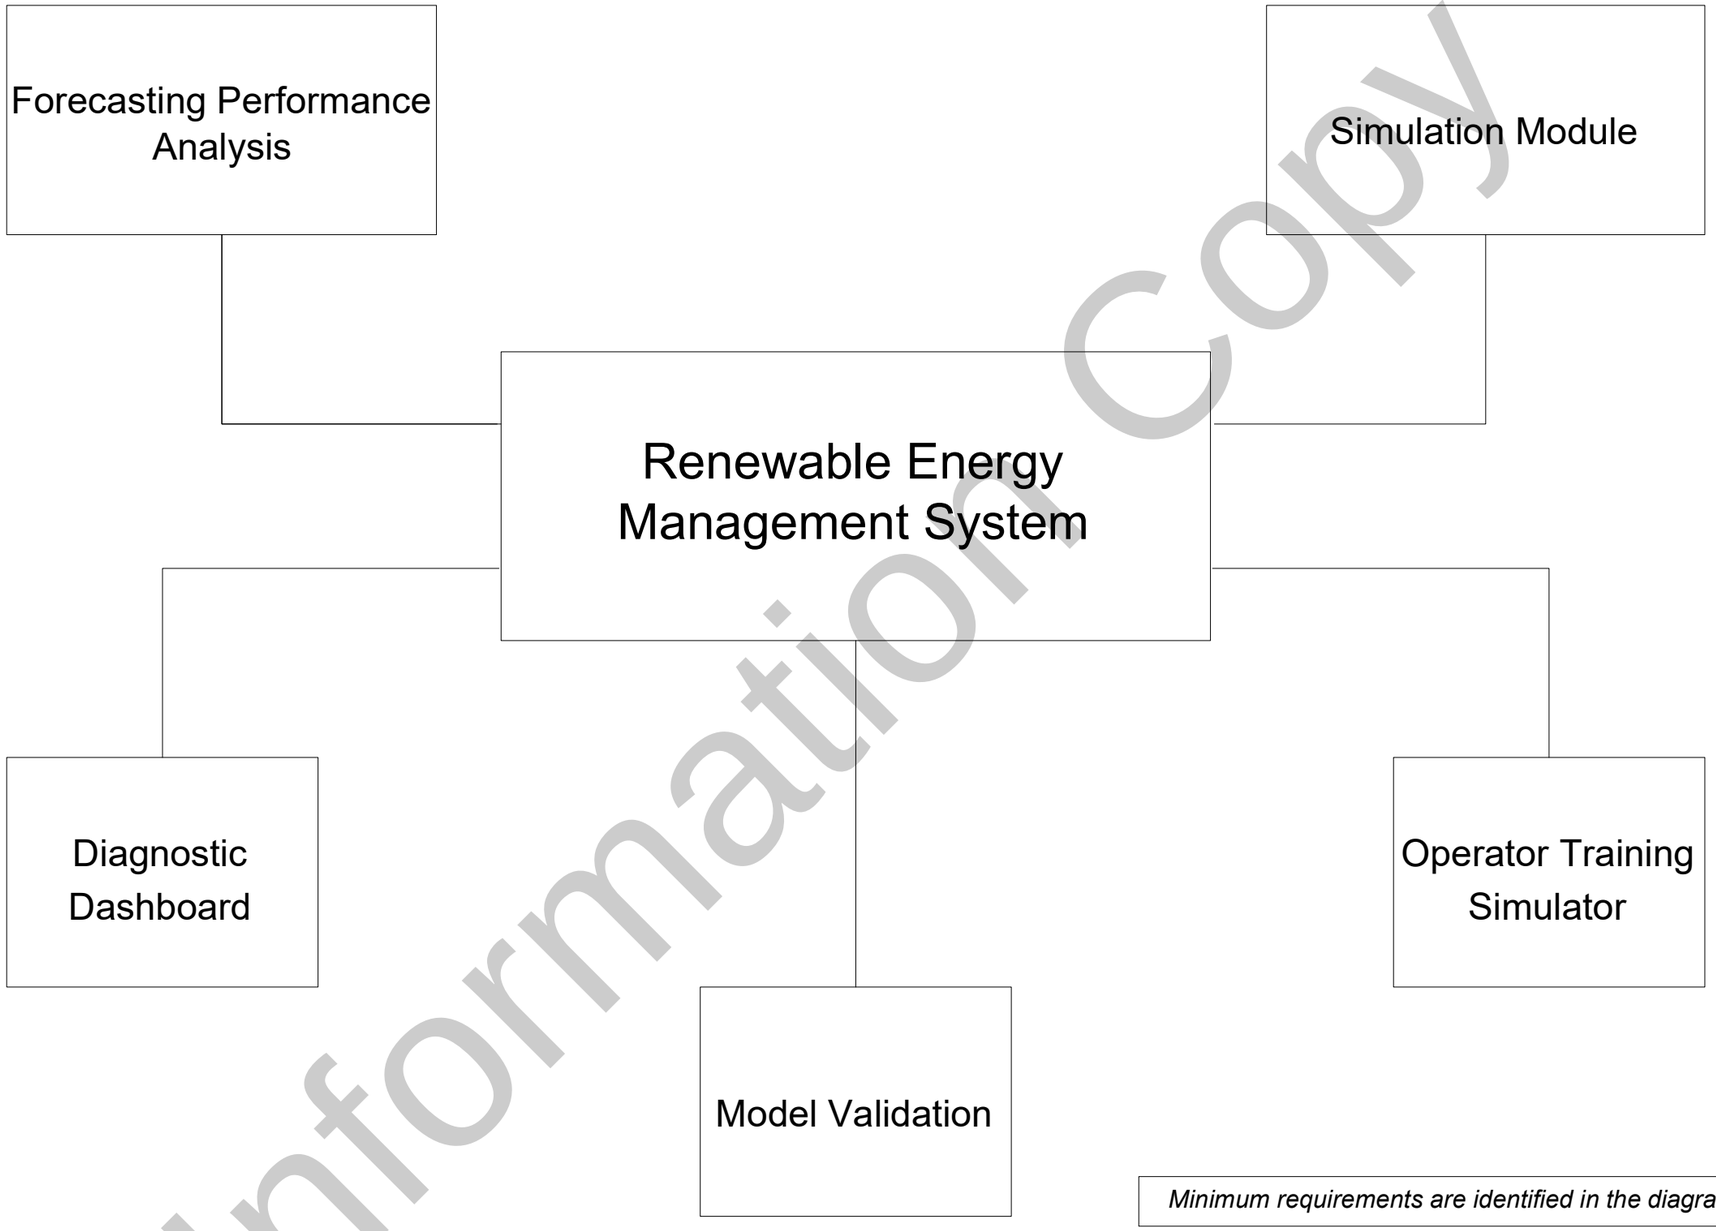

Minimum requirements are identified in the diagrams.

Information Copy

Property of NTNSP Director Engineering

Property of NTNSP Director Engineering

Revision Record					
Rev. No.	Date	Description	Drawn	Checked	Approved

NTNSP NATIONAL TRANSMISSION NETWORK SERVICE PROVIDER (PRIVATE) LIMITED

NATIONAL TRANSMISSION NETWORK SERVICE PROVIDER (PVT) LTD
DIRECTOR ENGINEERING

Project Title
POWER SYSTEM STRENGTHENING AND RENEWABLE ENERGY INTEGRATION PROJECT (PSSREIP) PACKAGE 6

Funding Agency
ADB

Drawing Title
SUPPORTING TOOLS & SIMULATION SYSTEM FOR REMS

Scale - NTS			Rev. Date		
Size - A3					
Sheet 01 of 01			Rev. 0		
Dwg. No. TD/CE/1/273/D/15					

	Signature		Date
Drawn	Sandamali		18.03.2026
Designed	Kasun		
Checked			
Approved			

Released for: Tendering ✓ ; Construction

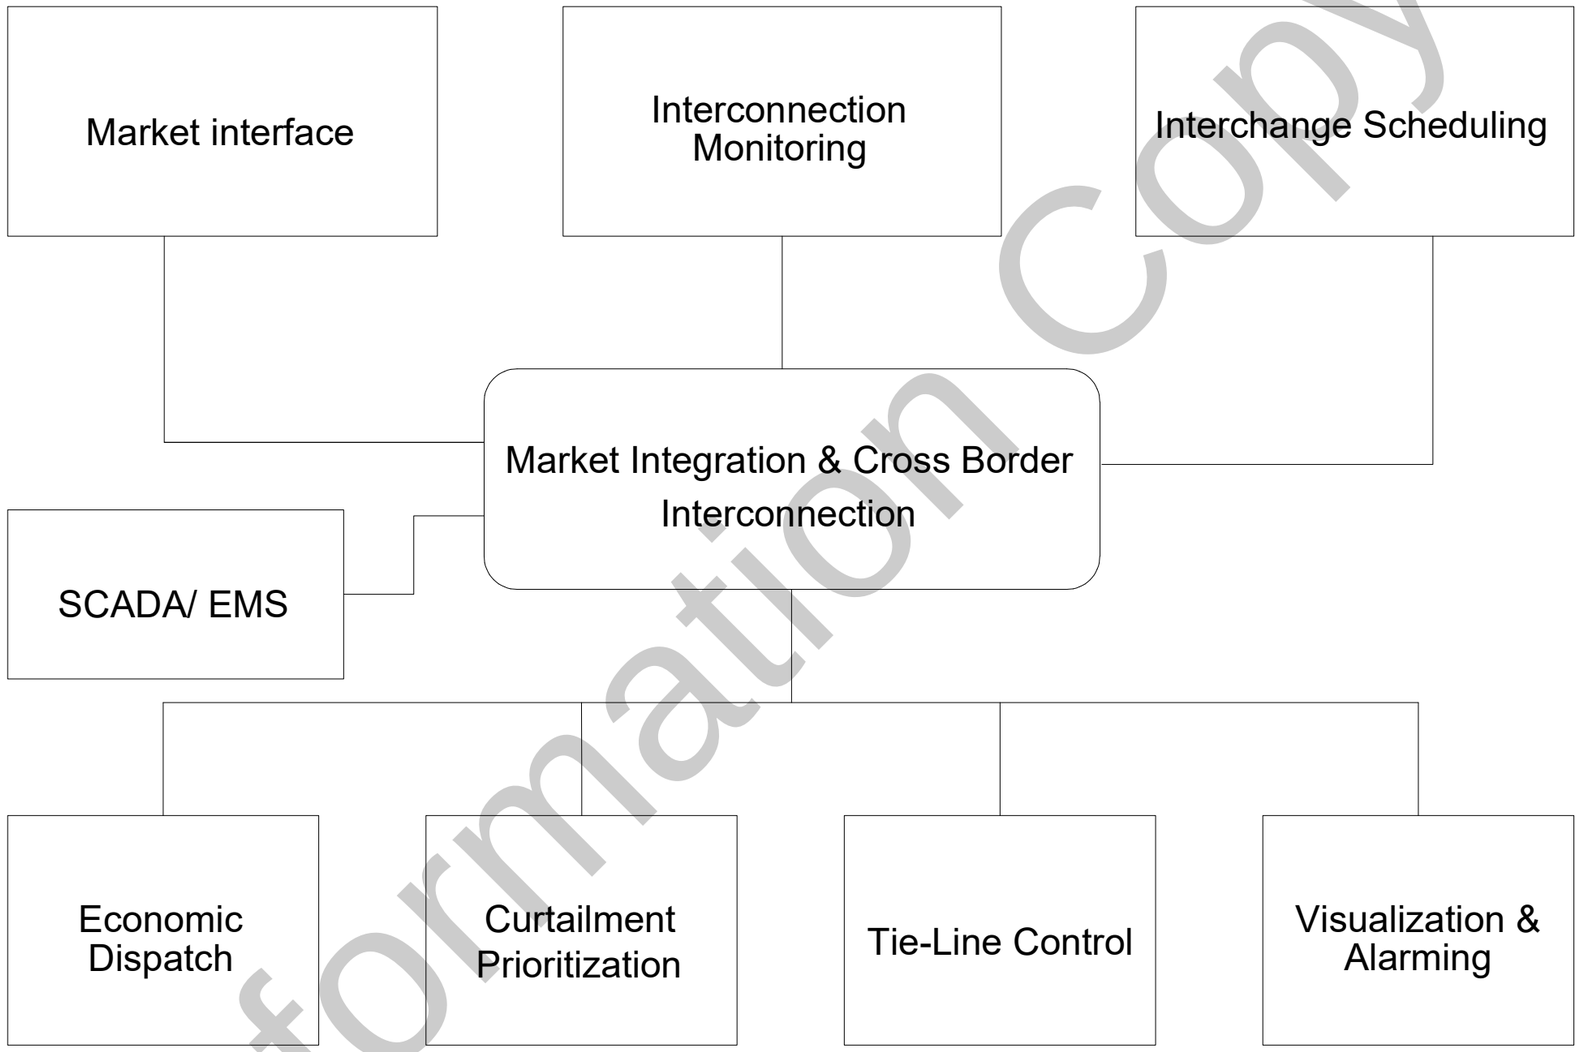

Minimum requirements are identified in the diagrams.

Information Copy

Property of NTNSP Director Engineering

Property of NTNSP Director Engineering

Revision Record					
Rev. No.	Date	Description	Drawn	Checked	Approved

NTNSP NATIONAL TRANSMISSION NETWORK SERVICE PROVIDER (PRIVATE) LIMITED

NATIONAL TRANSMISSION NETWORK SERVICE PROVIDER (PVT) LTD
DIRECTOR ENGINEERING

Project Title
POWER SYSTEM STRENGTHENING AND RENEWABLE ENERGY INTEGRATION PROJECT (PSSREIP) PACKAGE 6

Funding Agency
ADB

Drawing Title
PROVISIONS FOR MARKET INTERGRATION & CROSS-BORDER INTERCONNECTION

Scale -	NTS			Rev. Date	
Size -	A3				
Sheet	01	of	01	Rev.	0
Dwg. No.	TD/CE/1/273/D/16				

		Signature	Date
Drawn	Sandamali		18.03.2026
Designed	Kasun		
Checked			
Approved			

Released for		
	Tendering	✓
	Construction	

8000

2250

Date DD/MM/YYYY	Time HH:MM	DAY DDD		Dispatchable Generation	Gross Generation	ACE	Generation Deficit

Transmission System Overview Diagram

System Gross Generation and Dispatchable Generation Graph with Actual and Forecast (6hrs +)

Solar FC+ Actual Graph	Wind FC+ Actual Graph	Mini Hydro FC+ Actual Graph	Other RE FC+ Actual Graph

NCRE Generation Actual and Forecast (6hrs +)

Power System Security Analysis Alarms	StatCom, VSR, BESS, SynCon, Related Alarms NSCC System Alarms System Related Past Data	System Voltage Display	Reservoir Information Display

	Frequency 1	Frequency 2	Frequency 3	Frequency 4	Frequency 5	Frequency 6		

Minimum requirements are identified in the diagrams.

Information Copy

Property of NTNSP Director Engineering

Property of NTNSP Director Engineering

Revision Record

Rev. No.	Date	Description	Drawn	Checked	Approved

NTNSP NATIONAL TRANSMISSION NETWORK SERVICE PROVIDER (PRIVATE) LIMITED

NATIONAL TRANSMISSION NETWORK SERVICE PROVIDER (PVT) LTD
DIRECTOR ENGINEERING

Project Title: ***POWER SYSTEM STRENGTHENING AND RENEWABLE ENERGY INTEGRATION PROJECT (PSSREIP) PACKAGE 6***

Funding Agency: ADB

Drawing Title: OPERATIONAL DISPLAY OVERVIEW DIAGRAM

			Signature	Date
Scale - NTS	Rev. Date	Drawn	Sandamali	18.03.2026
Size - A3		Designed	Kasun	
Sheet 01 of 01	Rev. 0	Checked		
Dwg. No. TD/CE/1/273/D/17		Approved		

Released for: Tendering ✓ ; Construction

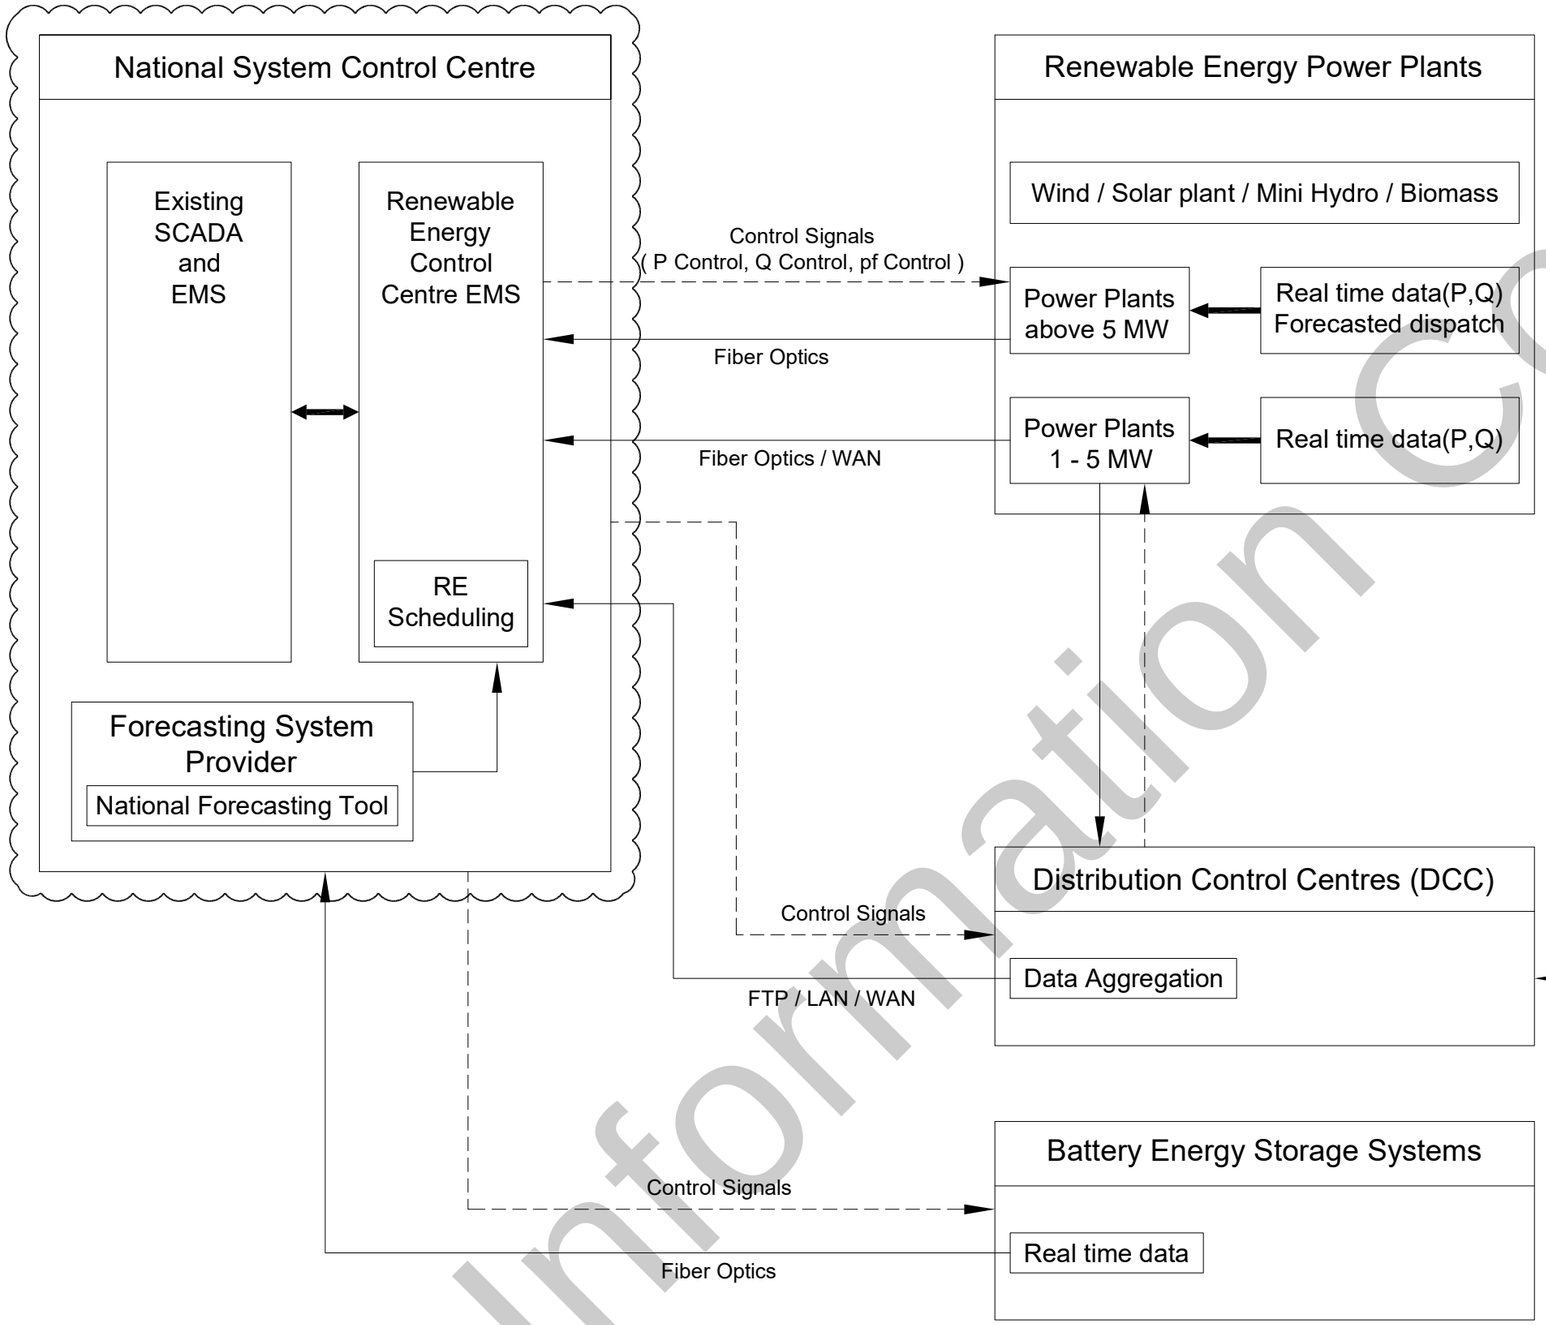

Note :-

1. Plants above 5MW via IEC 60870 – 5 – 104 protocol
   Controlling and Monitoring facility shall be available to NSCC. If this is connected to the 33kV feeder, monitoring facility shall be available to Distribution Control Center (DCC)s

2. Plants 1MW – 5MW via IEC 60870 – 5 – 104 protocol
   Monitoring facility shall be available to NSCC. Controlling and Monitoring facility shall be available to DCCs

3. Plants below 1 MW
   Aggregated value of MW and MVar shall be available to NSCC to monitoring purpose via DCCs. Controlling (Cluster Controlling) and Monitoring facility shall be available to DCCs.

4. Only the plants which are already connected to NSCC shall be integrated to the New REMS

5. Data Acquisition from each type of plants shall be via dedicated reliable communication media

6. All the data as per the data requirement shall be terminated to the CEB Communication Network or IT based cloud defined by the CEB, adhering to the Cyber Security Policy governed by the CEB and facilitating end to end protection up to the termination point. NSCC and DCCs will acquire the data from the termination location as per the protocols mentioned above and perform the controlling respectively. In case of an issue with monitoring or controlling due to the communication media, it will affect the financial implications for the plant.

7. Presently 05 Nos of DCCs have to be integrated and future provisions shall be kept for another 05 Nos of DCCs.

SCOPE

Information Copy

Property of NTNSP Director Engineering

Revision Record					
Rev. No.	Date	Description	Drawn	Checked	Approved

NATIONAL TRANSMISSION NETWORK SERVICE PROVIDER (PVT) LTD
DIRECTOR ENGINEERING

Project Title: *POWER SYSTEM STRENGTHENING AND RENEWABLE ENERGY INTEGRATION PROJECT (PSSREIP) PACKAGE 6*

Funding Agency: ADB

Drawing Title: CONTROL AND MONITORING CONFIGURATIONS OF RE & BESS AT NSCC

Scale - NTS
Size - A3
Sheet 01 of 01 Rev. 0
Dwg. No. TD/CE/1/273/D/18

	Signature	Date
Drawn	Chaminda	18.03.2026
Designed	Kasun	
Checked		
Approved		

Released for: Tendering ✓ ; Construction